
3600 mm médiafal, a képhez javított íves forma



Kiválasztott C célkép - S16 Cam_02 V3.3 C v1

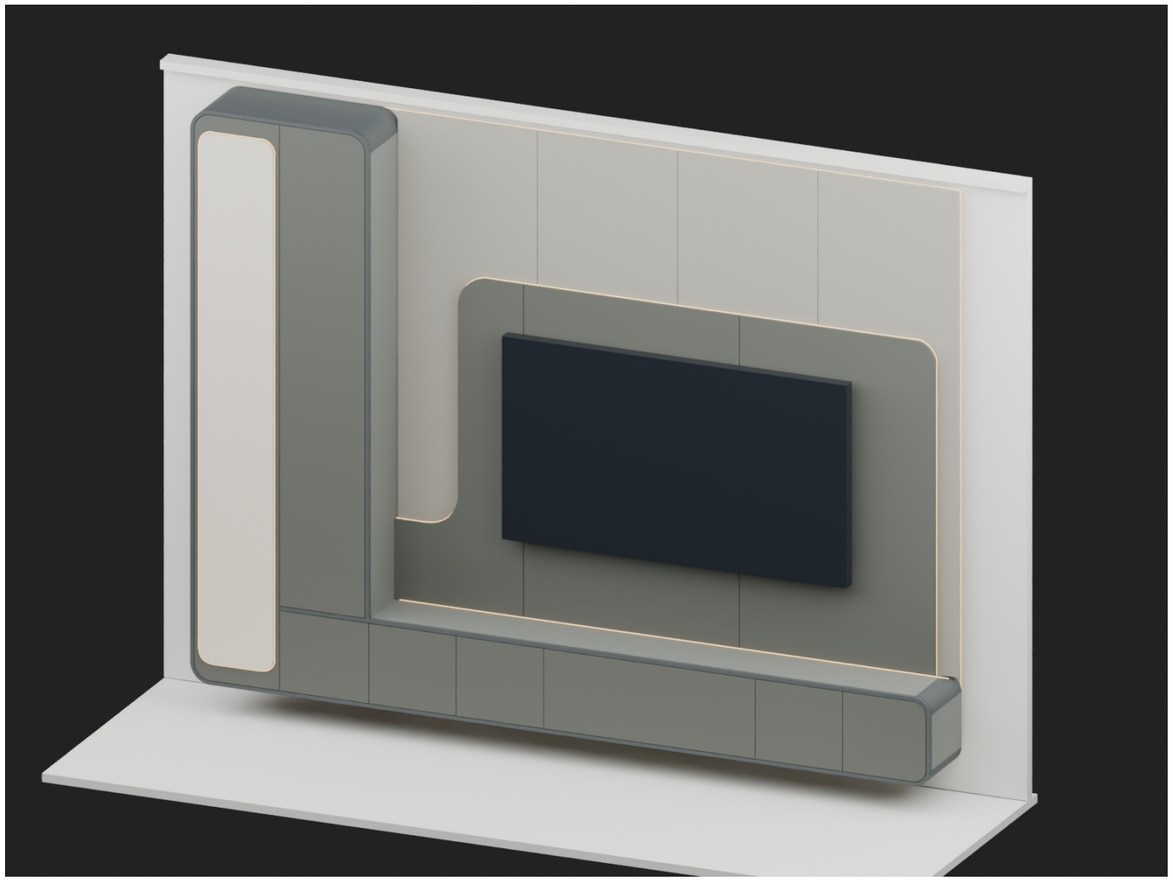

R05: tényleges 3D modell, műszaki stúdiónézet

A tulajdonos korrekciója alapján a TV-réteg a bal toronytól indul, ívesen felkanyarodik a képernyő mellé, és alul az alsó bútor fedlapjáig fut. R05:870mm torony,75col TV,25mm felső fényrés; bal fél alatt nincs fiók; teljes peremfény,105/105mm betétmargó; ezüstcsík nélkül.

Az új rádiuszok képre illesztett tervezési javaslatok: torony R100, alsó jobb sarok R80, textilbetét R60, TV átmenet R160/R140/R100. Ezeket nem állítjuk felmért képméretnek.

Becsült bruttó bútorár: 3 683 946 Ft; soronkénti sáv 2 736 612–5 183 707 Ft. S01 R16-hoz képest 714 646 Ft többlet. A két becslés sávja átfed.

Tartalom: hat magas nyomásra nyíló, csillapított fiók; két magas ajtó; tíz állítható polc; nyolc külön belső fényérzékelő. A frontosztás az összehasonlításhoz kidolgozott javaslat.

Állapot: rajzi és költség-előkészítés. Felmérés, anyag/ív/fény-minta, végleges vasalatfuratok, falrögzítés és műhelyi elsődarab még szükséges.

TERVEZÉSI JAVASLAT - NEM GYÁRTÁSI JÓVÁHAGYÁS

R05 – a teljes front hézagellenőrzése

Mi volt hibás?

A torony felső ajtóhézaga20mm volt. Az alsó bal front alatt5mm, a jobb szélső fiók ívénél helyenként1,07mm, a bal ajtó melletti osztólécnél1,5mm maradt. Ezek nem szerepelhettek volna ellenőrzött, egységes3mm-es részletként.

Mi változott?

A felső ajtóél17mm-rel feljebb, a bal ajtó alsó éle2mm-rel lejjebb került. Az alsó frontok Z171–549mm között futnak. Az alsó frontkeret18mm vastag; a jobb szélső fiókR59 a keretR62 belső ívében. Az osztóléc bal végeX436,5. A háttérpanel szélső illesztései is3mm-esek.

Mit ellenőriztünk?

Mind a8 nyíló front teljes kerületét0,5mm-es mintavétellel; az egyenes illesztéseket és az egyközpontú köríveket külön méretszámítással. Névleges hézag3mm. A poligon közelítés legkisebb eltérése0,001mm; a T-csatlakozásnál a legközelebbi sarok ferde távolsága3,34mm, a merőleges hézag ott is3mm.

Ütközés és mozgás

A120 bútoralkatrész7140 páros összevetésében nincs térfogati átfedés. Mind a6 fiók külön0–300mm mozgásánál nincs vizsgált ütközés. A névleges ajtóforgást az íves sapkák ellen is ellenőriztük1°-os és2mm-es mintavétellel, a kontúrcsúcsoknál is; találat nincs.

Megőrzött arányok

A TV mérete változatlan. A világos betét felső/alsó margója105/105mm, fényperemé100/100mm. A fényút a valódi ajtóhoronyban marad. A teljes panel feletti25mm mennyezeti LED-rés szándékos.

Az ellenőrzés határa


Ez a saját modell geometriai ellenőrzése. A felmért helyiség, tényleges pánt és kábelátvezetés, rögzítés, gyártási tűrések és villamos hőpróba még nem igazolt. A rajz továbbra sem gyártási kiadás. Részletes bizonyíték: audit/geometry_checks.json és motion_checks.json.

TERVEZÉSI JAVASLAT - NEM GYÁRTÁSI JÓVÁHAGYÁS

Homlokzat és fő méretláncok

870-es torony

Folytonos, háromrészes TV-réteg

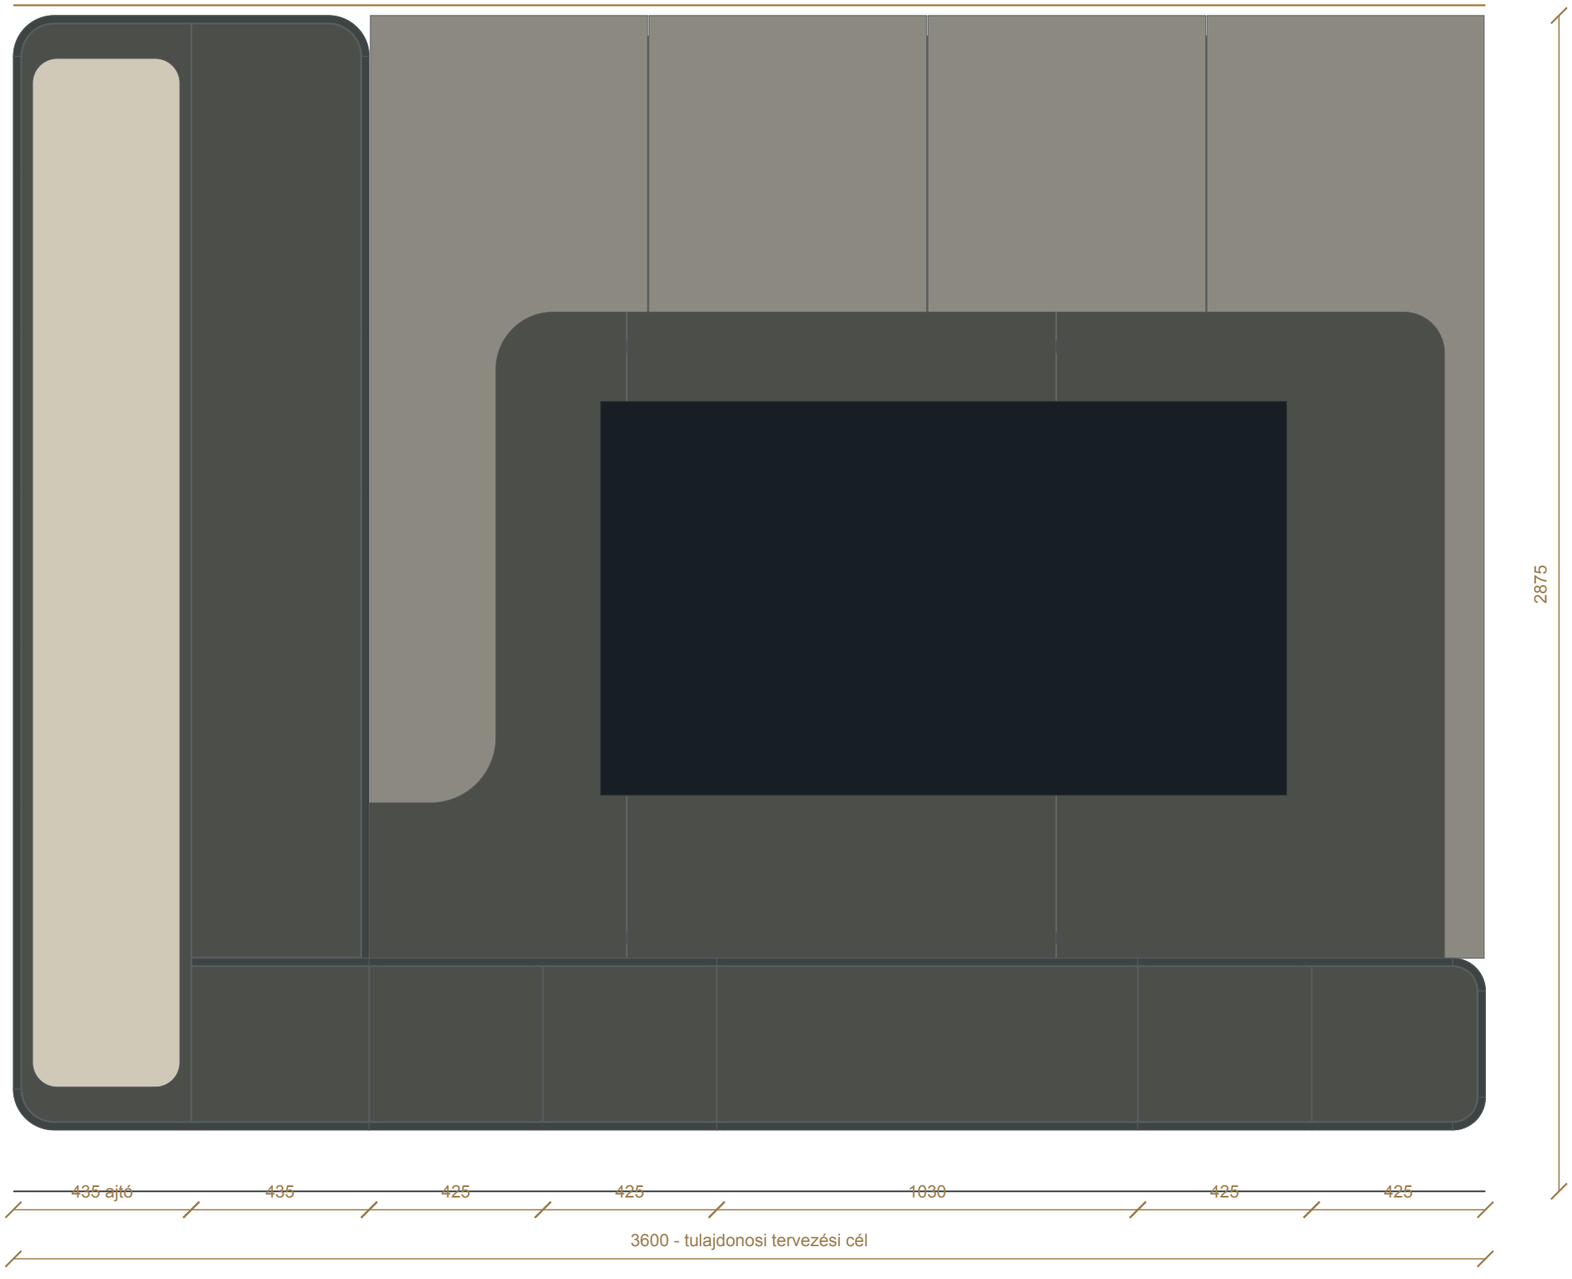

Befoglaló

3600 × 2875 mm. Korpusz/front 400 mm, textilbetéttel max.408 mm. Kész padló felett150 mm alsó él.

Alsó felső él

Minden alsó modul felső éle570mm. A torony jobb alsó sarka szögletes, folytonosan csatlakozik a fióksorhoz.

TV-réteg

X870–3500; Z570–2150. Y95–113; háttérfrontY78. Kiemelés35 mm. Nincs nyitott függőleges sáv a torony és a réteg között.

Szerelési hézag

3mm felső ajtóhézag is: keretR82/ajtóR79; a korábbi20mm rés javítva.3 mm front/panel közök,5 mm tervezett benyomási tér. Felső25 mm névleges rés nem helyszíni igazolás.

Rétegillesztések

TV-réteg3rész: LINK/MID/END. VarratX1500 és2550; cél a TV által részben takart hely. Valódi hézagot nem tüntetünk el.


Magassági forrás

Tulajdonosi25mm felső fényrés; v2b névleges2,90m; a legkisebb helyszíni érték és felállítás ellenőrizendő.

TERVEZÉSI JAVASLAT - NEM GYÁRTÁSI JÓVÁHAGYÁS

Az ívek és a folytonos réteg

TORONY OLDALA

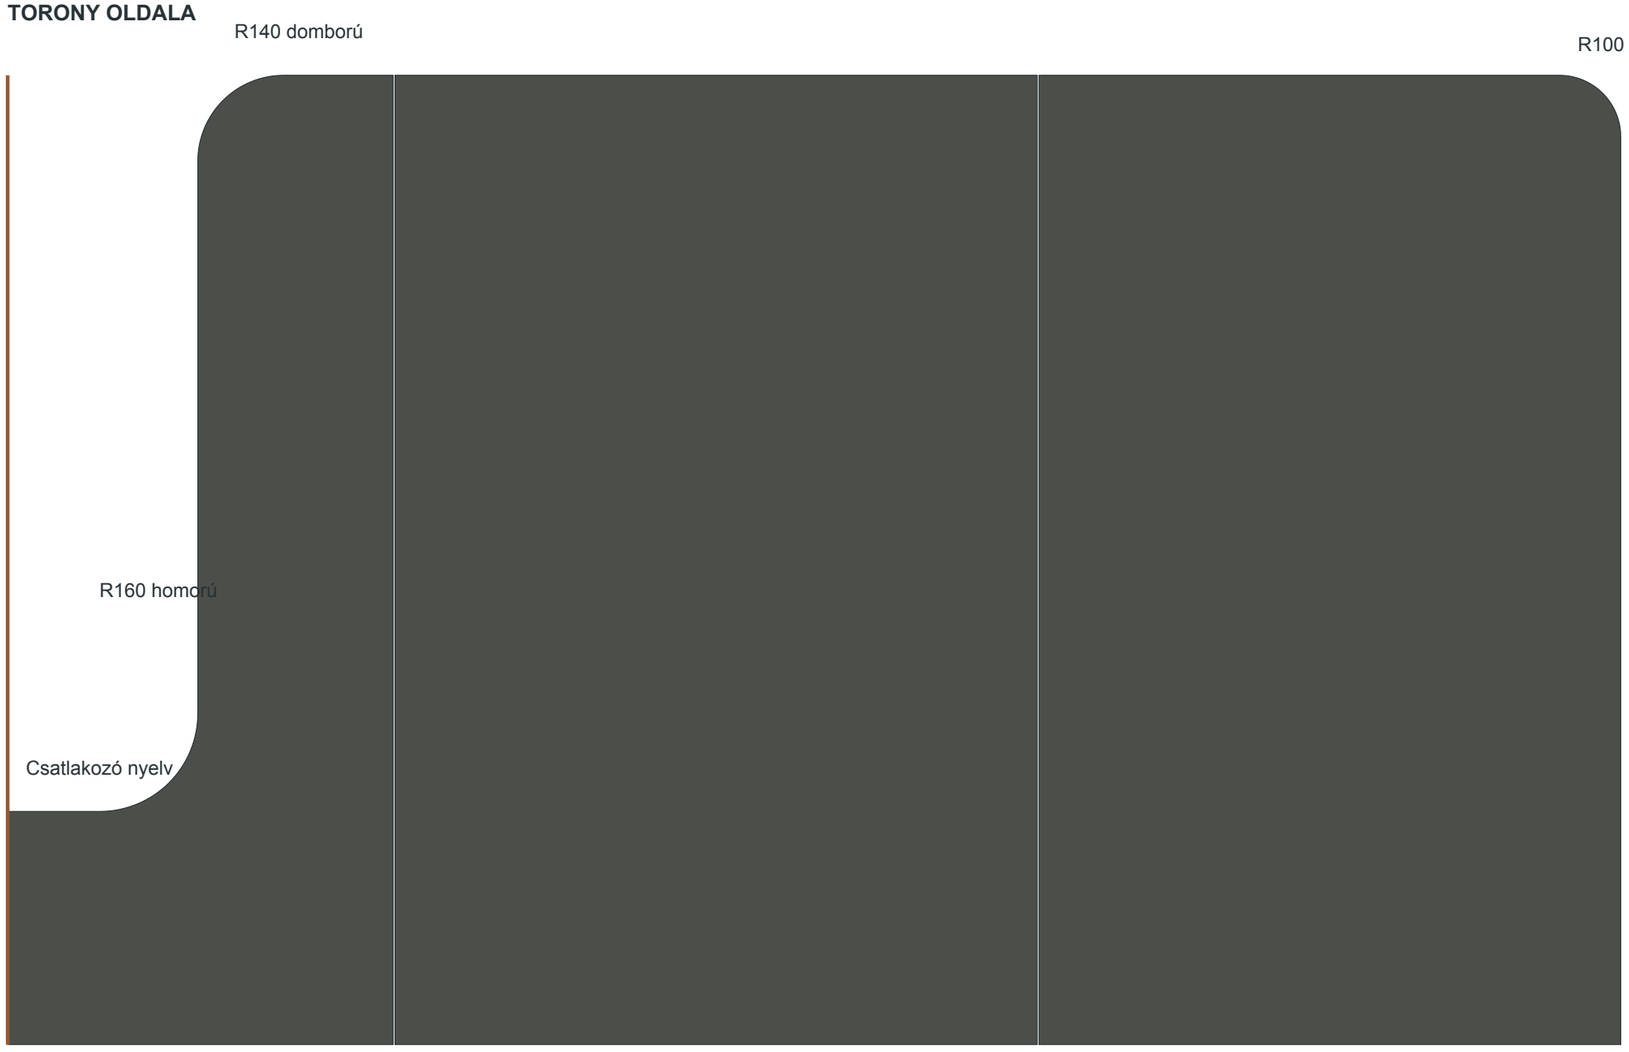

Alsó kontúr a bútor fedlapjáig: Z570. Nincs lebegő rés.

Rajzi kontúr nem darabolt ív

Az alkatrész-DXF-ekben és a DWG-ben az ívek körívként szerepelnek. A Blender megjelenítése sűrű háló; ez nem a gyártási kontúr felbontása.

A toronyR100 és az alsó sarokR80 saját belső ívvel rendelkező,18mm rétegvastagságú íves héj. Befoglaló mélysége337mm; nem337mm vastag MDF lap.

Kötelező1:1 sarokminta: külső ív, érintőleges átmenet, látszó hézag, élburkolat/festés, LED és az ajtó nyitása együtt.

R100 / R82 héj





Általános élletörés: csak finom R1–R2 tapintási él, mintával. Ez nem helyettesíti a nagy homlokzati rádiuszokat.

TERVEZÉSI JAVASLAT - NEM GYÁRTÁSI JÓVÁHAGYÁS

Belső kiosztás és nyitott állapot

Tíz polc: 406 × 290 mm

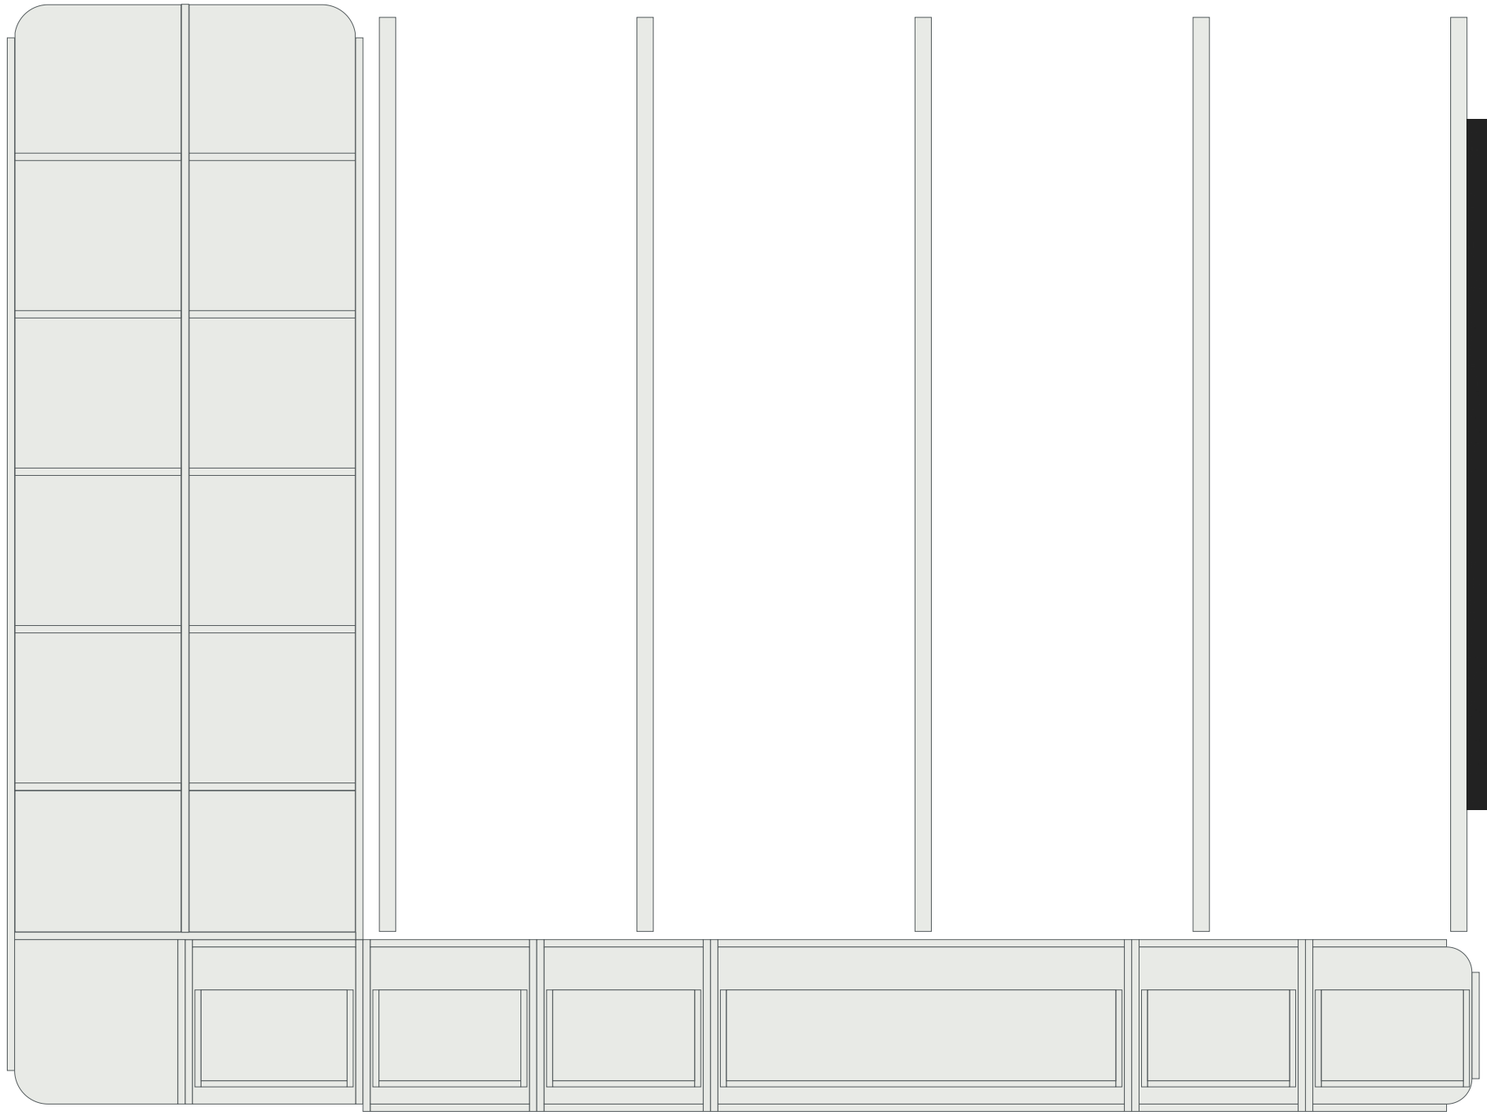

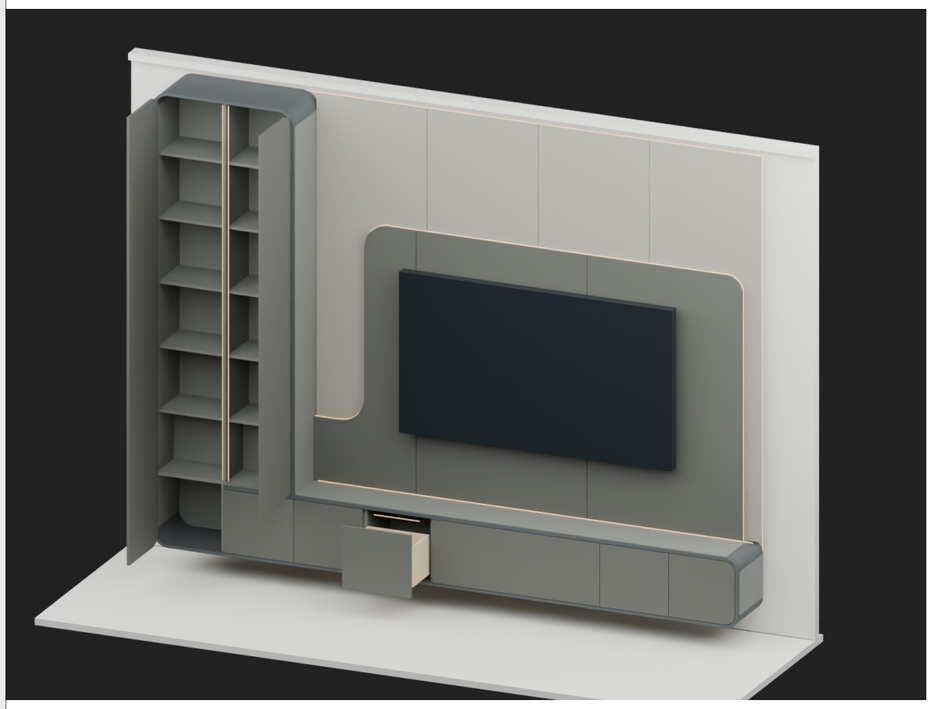


Hat fiók teljes kihúzása300mm. Nettó össztérfogat155,7liter; a S01 R16 értéke180,8liter. A bal fél alatt fiók helyett az aljáig nyíló szekrényajtó van. Doboz:15mm nyír, hasznos belmagasság222mm és mélység260mm.

A polcszám azonos, de a torony polcai406×290mm-esek,22,7%-kal szélesebbek a S01-nél. A nagyobb felső ív a legfelső rekesz külső sarkaiból helyet vesz el; a sarok környezetét nem számoljuk téglatestként szabad tárolótérnek.

Két alsó szervizrekesz mögött bontható elektronika

TERVEZÉSI JAVASLAT - NEM GYÁRTÁSI JÓVÁHAGYÁS

Alaprajz, kihúzás és használati sáv

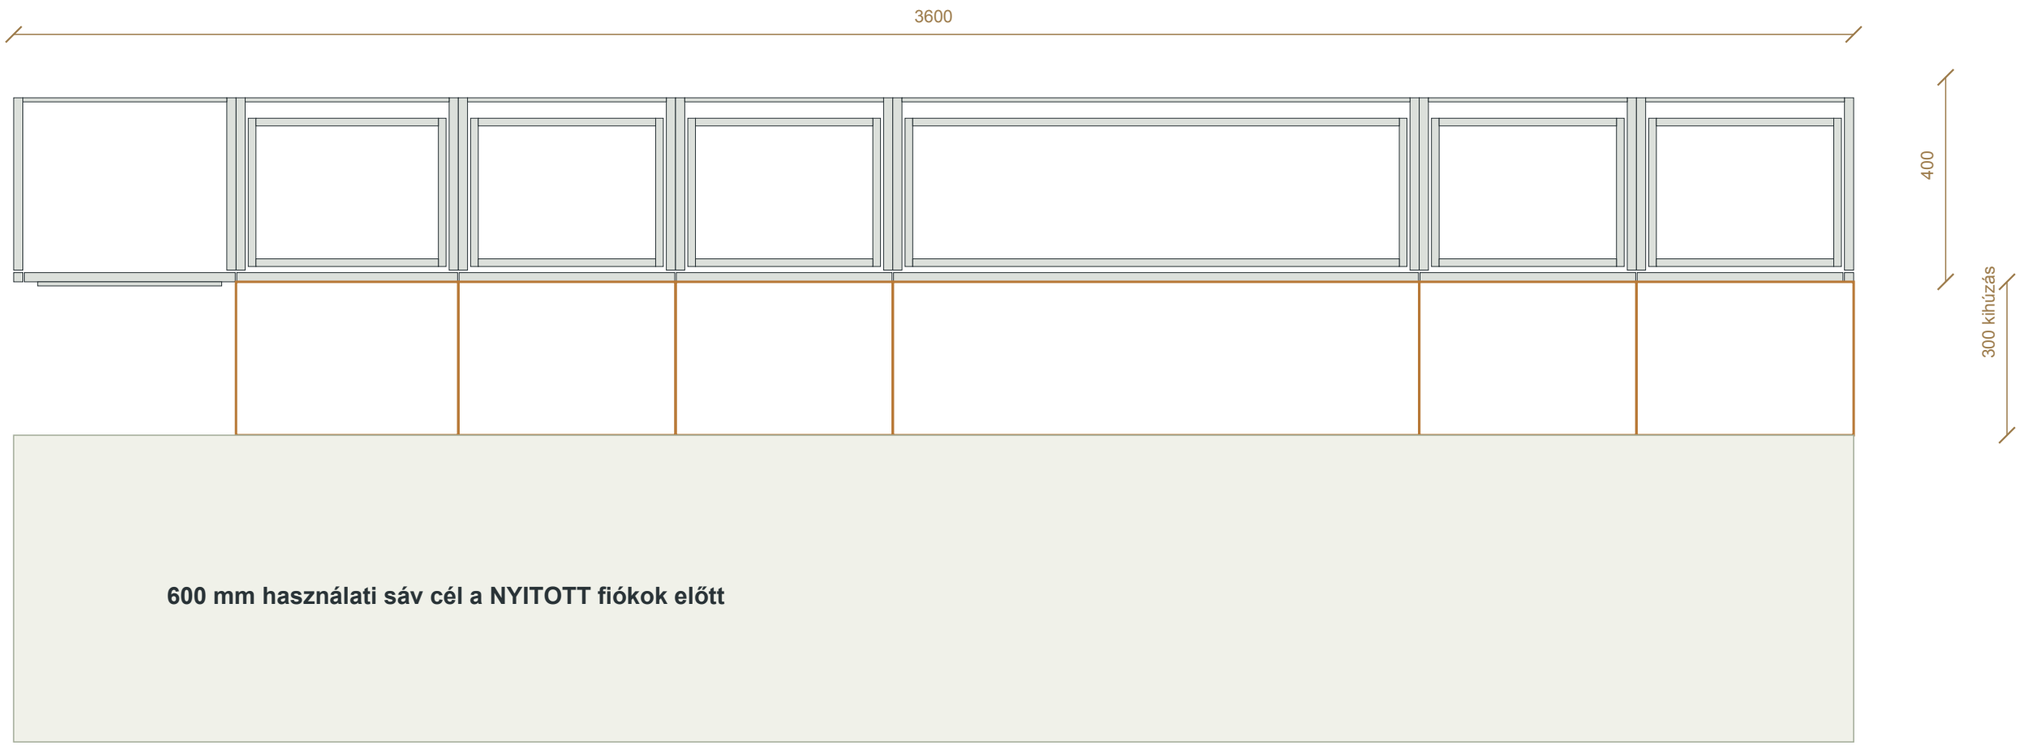

A szükséges szabad mélység a faltól:400mm bútor +300mm kihúzás +600mm használat =1300mm. Ez tervezési ellenőrzési sáv, nem igazolt helyszíni közlekedő.


A toronyajtók névleges90° nyitásánál kb.413mm előrenyúlással számolunk. A valós pántkinematika, textilbetét és szomszéd tárgyak mozgása külön sablonpróba.

S01-nél ismert asztal/fiók konfliktus volt. Az S16 dohányzóasztal pontos helye és a tényleges JÄTTEBO modulösszeállítás még nincs helyszínen rögzítve: nincs teljes szobai ütközésmentességi állítás.


W01 v2b falhossz4000mm. A3600mm bútorhoz kétoldalt200mm névleges hely marad; a javasolt kezdőpont világY4,25m. A függöny, nyíló teraszszárny, szegőléc és kiállások ezt még módosíthatják.

Metszetek, rétegrend és szerviz


A-A / TV-mező

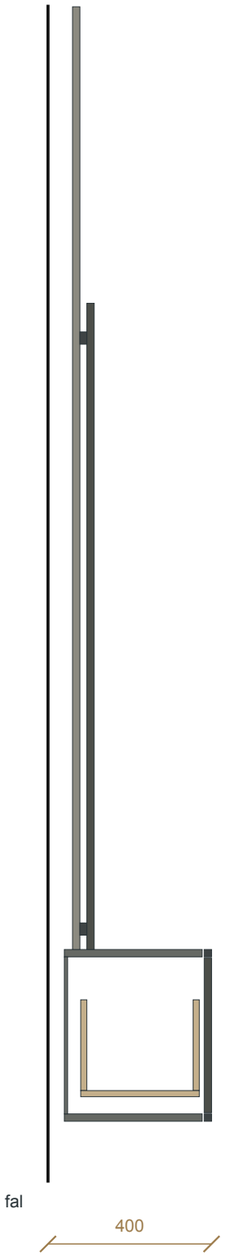

B-B / torony

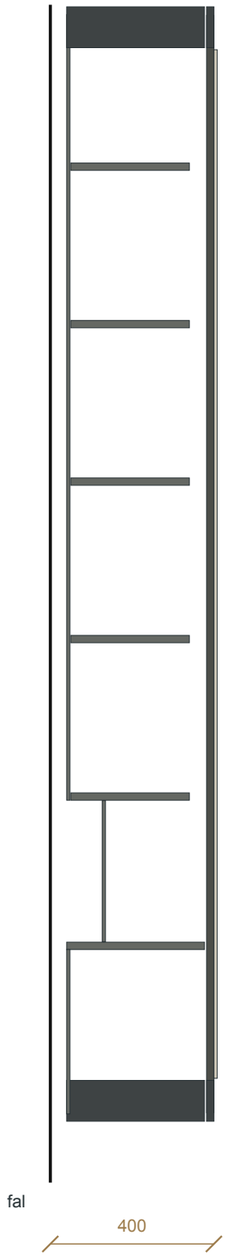

TV-mező vízszintes rétegrend

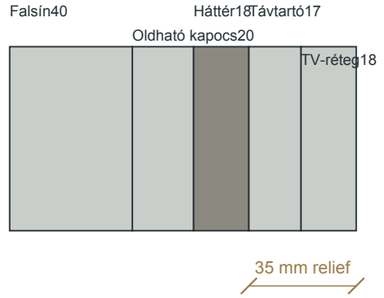

TV teherút: készülék -> saját VESA-konzol -> méretezett távtartó/teherhordó alátét -> igazolt fal. A18mm dekorpanel nem a TV teherhordó alapja. Konzolkivágás és távtartóhossz TV- és faladat után.

Torony alsó hátsó szerviz: Y40–135. Elölről kivehető406×345mm fedél; mögötte külön230V doboz és három DC-táp. A tárolásra maradó alsó rekeszmélység240mm.


Háttérpanel: elölről oldható kapocs kell. A25mm felső hézag miatt a hagyományos felfelé emelős akasztást nem tekintjük automatikusan szerelhetőnek.

Szellőzés: alsó és felső200×15mm rés/rekesz előirányzat, eltakarhatatlan kivitelben. A méretet a kiválasztott tápegységek vesztesége és teljes terhelésű hőpróba zárja le.

TERVEZÉSI JAVASLAT - NEM GYÁRTÁSI JÓVÁHAGYÁS

Világítás, betáp és hozzáférés

Külső 26.05 m + belső 6.83 m

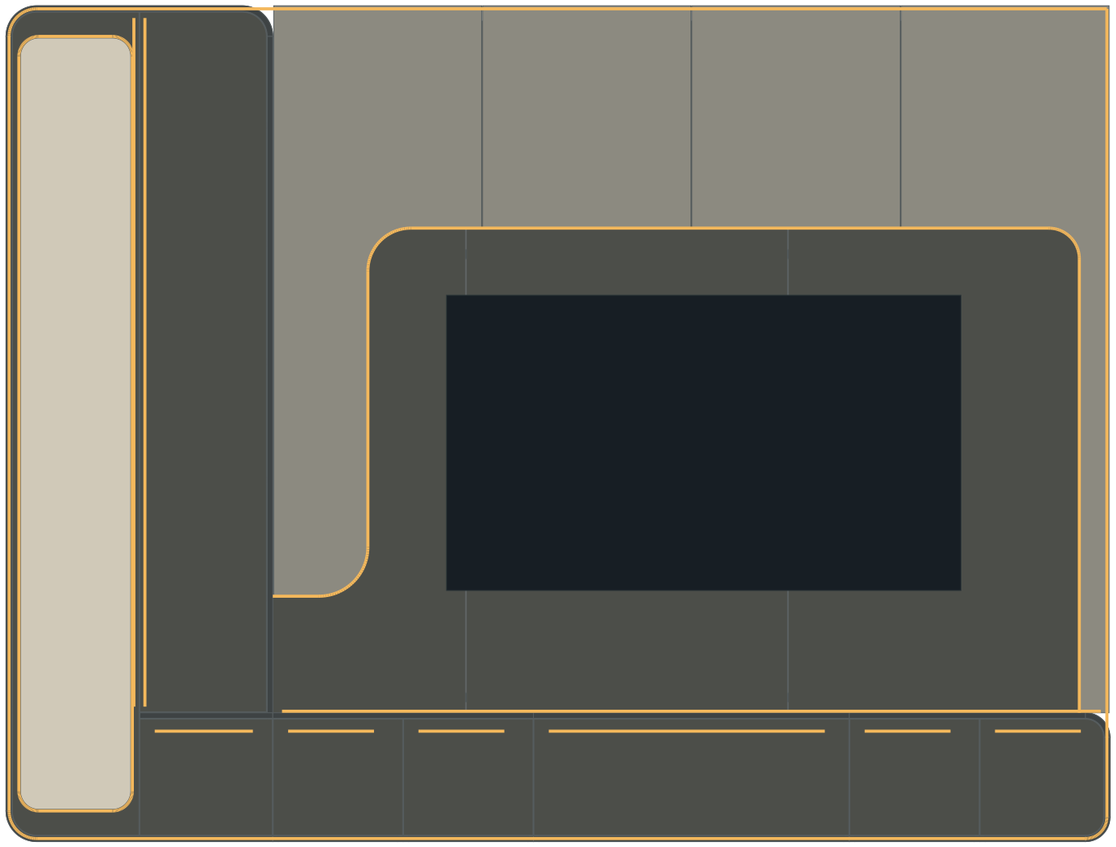

Ág	m	W	Táp / vezérlés
A1-OUTER-UP	8.791	87.91	PS1/Z1
A2-OUTER-LOW	3.671	36.71	PS2/Z2
A3-TV-CONTOUR	5.238	52.38	PS2/Z3
A4-TEXTILE-LOOP	5.678	56.78	PS1/Z4
A5-DECK	2.670	26.70	PS2/Z5
I-D1	0.320	1.54	PS3/S-D1
I-D2	0.280	1.34	PS3/S-D2
I-D3	0.280	1.34	PS3/S-D3
I-D4	0.900	4.32	PS3/S-D4
I-D5	0.280	1.34	PS3/S-D5
I-D6	0.280	1.34	PS3/S-D6
I-TL	2.245	10.78	PS3/S-TL
I-TR	2.245	10.78	PS3/S-TR

LED névleges összteljesítmény: 293.3 W

D16 meglévő betáp -> elkülönített230V csatlakozó -> PS1/PS2/PS3 -> ágankénti védelem -> CCT vezérlő / belső szenzor -> fix korpuszprofil. Tápkimenetek nem párhuzamosíthatók.

5 külső CCT vezérlő; PS1:200W, PS2:200W, PS3:60W jelölt. A gyártói csatlakozók, Hue párosítás,2200–2700K jelenet és hőpróba még nyitott.

Az íves TV-fényhez hajlítható megfelelő profil/hűtés vagy műhelyben igazolt szegmentált rendszer kell, folyamatos opál fedéllel. Ez új technológiai tétel, nem az eredeti3m Hue szalag ingyenes meghosszabbítása.

Nyitás és a világos betét teljes peremfénye

Rész	R05 kialakítás	Ellenőrzés
Világos betét	360×2515mm,R60;105mm felső és105mm alsó távolság a teljes külső szekrényhez. Bal ajtóval mozog.	A peremfény teljes zárt lekerekített kör, nem csak egy függőleges csík.
Peremprofil	370×2525mm középvonal, R65;10mm széles,6mm mély fészek az18mm ajtóban.	CAD-ben és a modellben külön mart fészek. A profil pontos mérete, hűtése és hajlíthatósága próbaminta után végleges.
Ajtó táplálása	24V CCT, rejtett pántoldali hajlításálló3eres átvezetés. Oldható csatlakozó, mindkét oldalon húzásmentesítés.	Nyitási íven túlvezetett laza hurok a pántok között; gyári kábel minimális hajlítási sugara, becsípődés és ismételt nyitáspróba. Méretezés nélkül nincs gyártási kiadás.
Ajtók	2×412,5mm széles, eltérő magasságú, rugó nélküli pánt +mágneses nyomásnyitó;bal6/jobb5pánt keret.	Nincs klasszikus fogantyú. Textilnél a merev ajtóperem a nyomási pont. Nyomóút és nyitási erő mintán ellenőrizendő.
Fiókok	6 magas front, MOVENTO300 +TIP-ON BLUMOTION. Nyomásra nyitás és csillapított záródás.	3mm frontköz,5mm tervezett benyomási tér; széles D1/D4 front szinkronnal és stabilizátorpróbával.
Külső keret	Fix fényudvar a teljes kompozíció körül,25mm mennyezeti rés.	A torony jobb alsó sarkán nincs önálló visszakerekítés; alul a fény a fióksorral együtt fut tovább.

Az ajtó és a fiók eltérő működésű: a fiók csillapított, az ajtónál a rugó nélküli nyomásnyitást terveztük. A nyitott modellen csak D3 fiók van kihúzva, a többi csukva; az ajtók névleges90°-ot szemléltetnek; a gyári pánt tényleges mozgását és a vezetéket műhelyi próbával kell igazolni.

TERVEZÉSI JAVASLAT - NEM GYÁRTÁSI JÓVÁHAGYÁS

75 colos TV: a tulajdonos méretkorrekciója

Adat	75col méretreferencia	Ellenőrzés / határ
Készülék	Samsung QE75Q7FAAUXXH	A65colos előző helyfoglalót váltja ki. A család méretsorában65 után75col következik.
Talp nélküli méret	1677,5 ×962,4 ×61,1mm	Gyári HU specifikáció,2026.10.29. Nem arányosan felszorzott65colos test.
Tömeg / VESA	25,3kg /400×400mm	VESA magassági eltolás, csavarhossz és távtartó a valós szerelési rajz szerint.
TVM3605 konzol	40–100col; max75kg; max600×400 VESA	A75colos referencia névleg belefér. Ez nem a falhorgony vagy a dekorpanel teherbírásának igazolása.
Hely a képernyő körül	Fent218,8mm; fedlapig398,8mm	Jobbra386,25mm; a bal egyenes kontúrszakaszig256,25mm. A folytonos íves forma változatlan.
Képernyő középpontja	X2275 /Z1450mm	Szemmagasság és nézési komfort a tényleges kanapén próbálandó.
TV árkeret	350000Ft becslés;300000–450000Ft sáv	Régi KI-033 keret250000Ft; különbözet100000Ft. Nem írjuk hozzá a bútor3,68M keretéhez duplán.
Lakás75col TV-vel	27 026 836Ft	Csak W01 ésTV-csere utáni feltételes előirányzat;2M tartalék külön.

Forrás: https://www.samsung.com/hu/tvs/qled-tv/q7f-75-inch-qled-4k-smart-tv-qe75q7faauxxh/

Konzol: https://brandportal.vogels.com/m/76109be3bb82e160/original/3836050_TVM3600Series_Leaflet_Document_EN.pdf

Beszerzési státusz: a gyári oldalon a referencia nem eladó. A75col méret a terv része, a végleges készülék és ára külön beszerzési döntés. Nincs rendelés.

TERVEZÉSI JAVASLAT - NEM GYÁRTÁSI JÓVÁHAGYÁS

Anyagok és felületképzés

Kód	Anyag / felület	Konkrét megoldás és feltétel
M01	18 mm kétoldalt melaminos grafitszürke bútorlap	Korpusz és polc; gyártó/kód műhelyi egyeztetésre. ABS 1 mm a látszó élen. Közös S01 funkcionális tartalom
M02	18 mm MDF + kétoldali lezárás + szatén 2K PU grafit	R100 torony/R80 alsó fix keret és18mm rétegvastagságú laminált sarokhéj; NCS S7500-N induló színminta,10–15GU/60° cél. Nem autófesték-kód. Íves héj rétegrendje műhelyi mintával. Minta nappal és 2700 K fényben
M03	EGGER H3198 ST19 Dark Grey Fineline dekorjelölt	18 mm hordozón gyári dekor vagy kiegyenlített HPL-rétegrend; összvastagság kész 18 mm céltól eltérés esetén méretfrissítés. Erezet vízszintes fronton, függőleges TV-mezőn. Gyári dekorazonosság ellenőrizve, HU készlet/ár és minta nyitott
M04	18 mm MDF + finomszövésű szürke falburkolat	Háttér: textilhatású, nem kő és nem vastag kárpit. Vescom Bely+Print hordozócsalád jelölt; egyedi neutrális szürke próba, grafika nélkül. Ragasztó/hátoldali kiegyenlítés gyártói egyeztetéssel. Végleges szín/SKU nincs kiválasztva
M05	6 mm hordozó + vékony valódi elefántcsont szövet	6mm hordozó +vékony valódi szövet;360×2515mm bontható ajtóbetét,R60; kész8mm céltól eltérés a geometriát módosítja. Kárpitos szövet/ragasztó és ajtótömeg-próba kell
M07	15 mm nyír rétegelt lemez, matt vízbázisú lakk	Fiókdobozok; csiszolt élek, kész vastagság mérendő. Fenék 15 mm, oldalak 15 mm. Blum max.16 mm oldalfal alatt
M08	8 mm grafit hátlap	Korpuszhátak, bontható szervizajtók; élek zárva. Tervi anyag

R05 változás: a M02 íves sarokhéjak18mm kész rétegvastagságú, rétegelt/lamellázott szerelvények. A118-as R01 laplista nem érvényes. A sarkok nem sűrű sokszögként gyártandók. Mintázat: visszafogott szürke fa, grafika nélkül; a meleg esti fény nem barna festékkód.

TERVEZÉSI JAVASLAT - NEM GYÁRTÁSI JÓVÁHAGYÁS

Tételes költségbecslés 1/2

Kód	Tartalom	Mennyiség	Alap Ft	Alsó Ft	Felső Ft
C01	6 korpusz + sík dekorfront	1 csomag	225 000	175 000	305 000
C02	MOVENTO300 sínpár	6 pár	210 000	168 000	276 000
C03	TIP-ON + kapocs + szinkron + stabilizátor	6 szett	180 000	144 000	240 000
C04	6 nyír fiókdoboz	1 csomag	135 000	100 000	190 000
C05	Alsó bútor műhelymunka	1 csomag	200 000	160 000	240 000
U01	Háttér hordozó MDF	6.25807 m²	78 226	59 452	106 387
U02	Szürke textilhatású háttér, beszerzési keret	6.93 m²	166 320	110 880	249 480
U03	Toronytest, 10 polc, bontható hátak	1 csomag	155 000	120 000	220 000
U04	2 ajtó dekorral + pánt/TIP-ON	1 csomag	190 000	145 000	265 000
U05	Nagy ívű grafit keretek és laminált sarokhéjak	1 csomag	285 000	195 000	430 000
U06	Folytonos TV-réteg és távtartók	4.16 m²	145 600	104 000	208 000
U07	Valódi textilbetét, bontható rögzítés	1 db	46 000	31 000	71 000
U09	Felső műhely-összeállítás és segédanyag	1 csomag	100 000	75 000	150 000
U10	Együttes szín-/él-/fénypróba	1 csomag	65 000	45 000	100 000
F01	7 korpusz rögzítése és helyszíni beépítés	1 csomag	504 800	429 080	656 240

Árállapot: minden új S16 tétel bruttó tervezői becslés,2026.10.29.; nincs írásos ajánlat vagy igazolt magyar webshopár. Az Excelben a mennyiség és egységár külön szerkeszthető; a csomagok tartalmi lehatárolása és forrása mellettük olvasható.

TERVEZÉSI JAVASLAT - NEM GYÁRTÁSI JÓVÁHAGYÁS

Tételes költségbecslés 2/2

Kód	Tartalom	Mennyiség	Alap Ft	Alsó Ft	Felső Ft
F02	Plusz előre oldható panelkapcsok/sínek	1 keret	60 000	35 000	95 000
TV01	Vogel TVM3605 konzol	1 db	32 000	27 200	41 600
L01	Belső világítás teljes 8 érzékelős csomag	1 csomag	196 000	135 000	292 000
L02	24V CCT külső LED beszerzés	30 m	210 000	135 000	300 000
L03	Külső profil, opál fedél, végzáró	30 m	135 000	90 000	195 000
L04	CCT vezérlők, 5 független külső fényút	5 db	95 000	70 000	140 000
L05	Külső 24V/200W tápegység	2 db	70 000	50 000	100 000
L06	Külső kábel, védelem, csatlakozók	1 csomag	50 000	35 000	80 000
L07	Belső kompatibilis 24V/60W táp	1 db	25 000	18 000	38 000
L08	Külső villamos szerelés és hő/fénypróba	1 csomag	90 000	60 000	140 000
L09	Torony szerviztér kialakítása	1 csomag	35 000	20 000	55 000

Összesen	Alap Ft	Alsó Ft	Felső Ft
S16 R05	3 683 946	2 736 612	5 183 707

Árállapot: minden új S16 tétel bruttó tervezői becslés,2026.10.29.; nincs írásos ajánlat vagy igazolt magyar webshopár. Az Excelben a mennyiség és egységár külön szerkeszthető; a csomagok tartalmi lehatárolása és forrása mellettük olvasható.

TERVEZÉSI JAVASLAT - NEM GYÁRTÁSI JÓVÁHAGYÁS

S01 / S16 összevetés és feltételes lakáskeret

Feltétel	S01 Kyoto Ink R16	S16 Monza Magno R05
Szélesség	3600mm	3600mm
Fiókok / nyitás	6 magas, MOVENTO300 +TIP-ON BLUMOTION	6 magas, külön nyitású;155,7liter, eltérő szélességek
Fióktérfogat	180,8liter	155,7liter;−13,9%;bal alsó rész helyette szekrényrekesz
Torony	2ajtó,10polc331×290mm	2ajtó,10polc406×290mm;22,7%-kal szélesebb polcok
Belső fény	8 külön érzékelő,7,25m LED	8 külön érzékelő,6,83m LED
Külső fény	8,50m,3fényút	26.05m,5fényút
Alapbecslés	2 969 300Ft	3 683 946Ft
Becslési sáv	2 438 726–4 030 447Ft	2 736 612–5 183 707Ft

A feltételes lakáselőirányzat:26 212 190 -2 969 300 +3 683 946 = 26 926 836 Ft. Ez kizárólag a W01 médiafal cseréje, nem a teljes S16 lakás költsége.

A18 000 000Ft cél feletti összeg 8 926 836Ft. A2 000 000Ft tartalék külön marad; a keretet nem emeltük meg.

Az S16 alsó fiókos rész950 000Ft, a közös rögzítési alap504 800Ft, a TV-konzol32 000Ft a S01-ből induló összehasonlító feltevés; a fiókos rész az eltérő szélesség miatt korrigált. Az S16 íves héjak, rétegelt háttér és több fényút külön többlet.

TV-készülék, közös szállítás/felhordás/daruzás és más szobai tárgyak nem részei ennek az öt csomagsornak. A meglévő lakáskeret KI-151/KI-137 soraiban maradnak; nem nullaköltségűek.

Szerelési/műhelyi átfedés: KI-014 és KI-106 a végső ajánlatban egyeztetendő. Az eredeti négyajtós kisebb promptbútor nem közvetlen árversenytárs. Második stílus nincs megadva.

TERVEZÉSI JAVASLAT - NEM GYÁRTÁSI JÓVÁHAGYÁS

Vasalatok, kötés és szerelési sorrend

Rész	Kidolgozott javaslat	Még szükséges igazolás
Fiókok	760H3000S 300mm sínpár;T51.7601 kapocspár;T60L7040 S0 vagyT60L7140 S1;T60.1125W szinkron LW-267.	S0≤10kg/S1>10–20kg teljes fióktömeg. A40kg sínterhelés nem helyettesíti a TIP-ON működési tartományt. Széles/rövid D4 stabilizátorpróba.
Doboz	SKW=LW-42; SKL=300-10=290. 15mm oldalak,260mm nettó mélység,222mm nettó magasság.	Blum T65.1000.02 sablon, pontos kapocs/kampó/alákivágás. Saját CNC-koordináta nincs kitalálva.
Toronyajtó	bal6/jobb5pánt költségkeret; rugó nélküli inset CLIP top +mágneses TIP-ON; a textil és teljes peremfénye a bal ajtóval mozog, rejtett24V átvezetéssel.	Pontos cikkszám/talp, ráütés, csészetávolság és ajtótömeg műhelyi lezárásra. Az ajtócsillapítás nincs állítva.
Rögzítés	7 korpuszra S01 minőségű Camar-rendszer költségelőirányzat; panelre elöl oldható rejtett kapocs.	Falanyag, vezetékkeresés, üres/teli tömeg és kihúzási nyomaték után pontos rögzítési terv. Nem univerzális tiplikiosztás.
Íves héj	R100/R82 torony ésR80/R62 alsó sarok;18mm rétegvastagság,337mm mély egyedi szerelvény.	Ragasztott lamellák/hajlítható rétegelt lemez technológiája; rugóvisszaalakulás, sablon és felületminta.

1. Felmérés és D16–18/G kiállások közös koordinátájú rögzítése; fal és szerelőút igazolása.

2. Falsínek és korpuszok szintezése; a torony helyszíni összeépítése. Az íves héjakat a korpusz után, oldható kötéssel rögzítsék.

3. Tápkörök, hozzáférhető szerviz és hőpróba; bontható hátak, majd háttérpanelek.

4. TV teherhordó konzol és átvezetések; kontúrozott háromrészes réteg; fiókok/ajtók, világítás és hézagok beállítása.

5. Teljes elsődarab- és használati próba, terhelés, nyitás, fény, szerviz. Csak ezután gyártásra kiadás.

TERVEZÉSI JAVASLAT - NEM GYÁRTÁSI JÓVÁHAGYÁS

Felmérési és jóváhagyási nyilvántartás 1/2

Kód / nyitott adat	Felelős	Elfogadási feltétel	Határ
G01 Felmérési minimumok és falsík	Asztalos felmérő	3 magasságban szélesség, 5 ponton magasság, átlók, faleltérés, szegő/függöny; közös XYZ fotóval	Gyártási méretkiadás előtt
G02 3600-as új frontosztás és870-es torony	Péter + tervező	Célkép és R05 homlokzat összevetése; hatfiókos funkció elfogadása	Árajánlat véglegesítése előtt
G03 Fal és függesztés	Asztalos + illetékes szakember	Falanyag/vezetékkeresés, terhek és horgony gyári méretezése, kihúzási teherpróba ha indokolt	Fúrás előtt
G04 Fiók működés és tömeg	Műhely + Blum szaktanácsadó	S0/S1 össztömeg; sablonfurat, min3mm rés; széles/rövid D4 stabilitás, egy teljes elsődarab	Sorozatgyártás előtt
G05 Ajtó/textil tömeg és nyitás	Műhely	Inset rugó nélküli pánt/talp/TIP-ON pontos SKU; bal6/jobb5pánt előirányzat terhelési igazolás; 90° mozgáspróba	Furatkiadás előtt
G06 Szín és rétegrend	Péter + asztalos/kárpitos	A3 együttminta nappali/2700K; él, ragasztó, lakk és textil	Felületgyártás előtt

Minden felsorolt pont állapota NYITOTT. Bizonyíték, jóváhagyó és dátum az Excel Lezárás lapján és a data/gates.json-ban rögzíthető. Nincs automatikus gyártási jóváhagyás. Nincs rendelés, ajánlatkérő levél vagy gépi futtatás.

Felmérési és jóváhagyási nyilvántartás 2/2

Kód / nyitott adat	Felelős	Elfogadási feltétel	Határ
G07 Fény és szerviz	Villanyszerelő	D16 kapacitás; végleges LED/profil/SKU/kapcsolás; Hue próba, teljes terhelésű hőpróba; vezeték/ágvédelem	Villamos kivitelezés előtt
G08 TV és kiállások	Felmérő + TV szerelő	Készülék/VESA magasság, csatlakozóhajlítás, feloldók, hűtés és D16–18/G pontok sablonja	TV-panelek kivágása előtt
G09 Szállítás, panelbontás	Asztalos/logisztika	Lift/ajtó/forduló mérés; helyszíni korpuszépítés; előrefelé oldható kapocs próbája 25mm mennyezeti résnél	Gyártás előtt
G10 Szobai használat és asztal	Péter + tervező	300mm fiókút után legalább600mm használati sáv cél; asztal tényleges helye, JÄTTEBO kézállás és nyíló teraszszárny	Végső elrendezés előtt
G11 Ajánlati átfedés és keret	Péter + ajánlatadó	F01/C05/U09 és KI-014; L08/KI-106; szállítás KI-151 és daruzás KI-137 egyeztetése	Rendelés előtt
G12 Műhelyi gép és gyártáskiadás	Műhely/gépkezelő	WOF211 megnevezés helyett adattábla, szerszám és befogás; sablonok/elsődarab. CNC-program nincs kiadva.	Gyártásra jóváhagyás előtt

Minden felsorolt pont állapota NYITOTT. Bizonyíték, jóváhagyó és dátum az Excel Lezárás lapján és a data/gates.json-ban rögzíthető. Nincs automatikus gyártási jóváhagyás. Nincs rendelés, ajánlatkérő levél vagy gépi futtatás.

Források, állományok és ellenőrzési határ

SRC01 C célkép + eredeti prompt

../sources/S16_Cam02_C_celkep.png

Pixelhash ellenőrizve; megjelenési referencia, nem felmérés.

SRC02 Blum 2026 online katalógus, MOVENTO rendelés

https://publications.blum.com/2026/catalogue/en/520/

760H3000S, T51.7601, S0/S1 működési tartomány, szinkron LW-267. Online oldal 2027/2028 felirattal; nem utólag igazolt termékár.

SRC03 Blum MOVENTO tervezés

https://publications.blum.com/2026/catalogue/en/521/

SKW=LW-42; SKL=NL-10; max16mm oldalfal; min2,5mm rés. Fúrás T65.1000.02 sablonnal.

SRC04 EGGER H3198 ST19

https://www.egger.com/en/furniture-interior-design/decors/H3198_19

Sötétszürke irányított fadekor, valódi minta szükséges.

SRC05 Sunricher CCT gyári leírás

https://www.sunricher.com/media/resources/manual/SR-ZG9101FA-CCT%20instruction%20V1.pdf

CV variáns 12–36V, 4×5A, 170×53,4×28mm; Hue kapcsolat külön próbálandó.

SRC06 Blum pántváltozatok

https://publications.blum.com/2022/catalogue/en/74/

Inset és rugó nélküli variáns külön termék. Pántszám/talp/furat nem kiadott.

SRC07 S01 R16 forrás

../../a902-s01-kyoto-ink-20261026/R16_feluletek_fiokok/data

Aktuális alkatrész/vasalat/fény geometria; élő regiszter öt sora visszaolvasva.

SRC08 Építészeti v2b modell

.wsg-inputs/03_blender/geometry_lock_A902_v2b.json

W01 tervi falsík 4m; 2,90m névleges belmagasság. Falminimum és szervizpontok helyszínen ellenőrizendők.

Aktív változat:R05_felso_ajtohezag. R01/R02/R03 elavult; R05 tartalmazza a tulajdonos szélesség-,75col TV- és világításkorrekcióját. A fő nézetek, DXF-alkatrészek, költségmodell és Blender ugyanebből az R05 adatmodellből készültek. A részletes ellenőrzések az audit mappában találhatók. A műhelyi sablonműveletek és CNC-programok nincsenek kiadva.

TERVEZÉSI JAVASLAT - NEM GYÁRTÁSI JÓVÁHAGYÁS

Alkatrészlapok 1–4

D1-L D1 korpuszoldal

337 × 402 × 18 mm

Anyag:M01; költség:C01

Szál:nincs

Nyers méret/művelet: műhelyi lezárásra.

Kontúr kész névleges méret. Vasalatfuratok gyári sablonnal.



U → ; V ↑ ; helyi (0,0) / mm

D1-R D1 korpuszoldal

337 × 402 × 18 mm

Anyag:M01; költség:C01

Szál:nincs

Nyers méret/művelet: műhelyi lezárásra.

Kontúr kész névleges méret. Vasalatfuratok gyári sablonnal.



U → ; V ↑ ; helyi (0,0) / mm

D1-T D1 fenék/tető


399 × 337 × 18 mm

Anyag:M01; költség:C01

Szál:nincs

Nyers méret/művelet: műhelyi lezárásra.

Kontúr kész névleges méret. Vasalatfuratok gyári sablonnal.

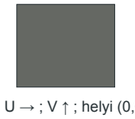

U → ; V ↑ ; helyi (0,0) / mm

D1-BACK D1 bontható hát


399 × 384 × 8 mm

Anyag:M08; költség:C01

Szál:nincs

Nyers méret/művelet: műhelyi lezárásra.

Kontúr kész névleges méret. Vasalatfuratok gyári sablonnal.

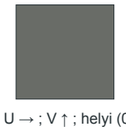

U → ; V ↑ ; helyi (0,0) / mm

TERVEZÉSI JAVASLAT - NEM GYÁRTÁSI JÓVÁHAGYÁS

Alkatrészlapok 5–8

D1-FRONT D1 egy magas front

432 × 378 × 18 mm

Anyag:M03; költség:C01

Szál:U vízszintes

Nyers méret/művelet: műhelyi lezárásra.

Névleges 3 mm frontköz; minimum benyomási út 2,5 mm. Korpusz elé 5 mm tervezett rés.



U → ; V ↑ ; helyi (0,0) / mm

D1-BOX-L D1 fiókoldal

290 × 237 × 15 mm

Anyag:M07; költség:C04

Szál:nincs

Nyers méret/művelet: műhelyi lezárásra.

Kontúr kész névleges méret. Vasalatfuratok gyári sablonnal.



U → ; V ↑ ; helyi (0,0) / mm

D1-BOX-R D1 fiókoldal


290 × 237 × 15 mm

Anyag:M07; költség:C04

Szál:nincs

Nyers méret/művelet: műhelyi lezárásra.

Kontúr kész névleges méret. Vasalatfuratok gyári sablonnal.

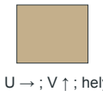

U → ; V ↑ ; helyi (0,0) / mm

D1-BOX-F D1 dobozelő/hát


357 × 222 × 15 mm

Anyag:M07; költség:C04

Szál:nincs

Nyers méret/művelet: műhelyi lezárásra.

Kontúr kész névleges méret. Vasalatfuratok gyári sablonnal.

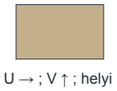

U → ; V ↑ ; helyi (0,0) / mm

TERVEZÉSI JAVASLAT - NEM GYÁRTÁSI JÓVÁHAGYÁS

Alkatrészlapok 9–12

D1-BOX-H D1 dobozelő/hát

357 × 222 × 15 mm

Anyag:M07; költség:C04

Szál:nincs

Nyers méret/művelet: műhelyi lezárásra.

Kontúr kész névleges méret. Vasalatfuratok gyári sablonnal.



U → ; V ↑ ; helyi (0,0) / mm

D1-BOX-B D1 fiókfenék

357 × 290 × 15 mm

Anyag:M07; költség:C04

Szál:nincs

Nyers méret/művelet: műhelyi lezárásra.

Kontúr kész névleges méret. Vasalatfuratok gyári sablonnal.



U → ; V ↑ ; helyi (0,0) / mm

D2-L D2 korpuszoldal


337 × 420 × 18 mm

Anyag:M01; költség:C01

Szál:nincs

Nyers méret/művelet: műhelyi lezárásra.

Kontúr kész névleges méret. Vasalatfuratok gyári sablonnal.

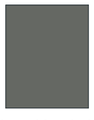

U → ; V ↑ ; helyi (0,0) / mm

D2-R D2 korpuszoldal


337 × 420 × 18 mm

Anyag:M01; költség:C01

Szál:nincs

Nyers méret/művelet: műhelyi lezárásra.

Kontúr kész névleges méret. Vasalatfuratok gyári sablonnal.

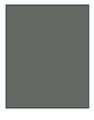

U → ; V ↑ ; helyi (0,0) / mm

TERVEZÉSI JAVASLAT - NEM GYÁRTÁSI JÓVÁHAGYÁS

Alkatrészlapok 13–16

D2-B D2 fenék/tető

389 × 337 × 18 mm

Anyag:M01; költség:C01

Szál:nincs

Nyers méret/művelet: műhelyi lezárásra.

Kontúr kész névleges méret. Vasalatfuratok gyári sablonnal.



U → ; V ↑ ; helyi (0,0) / mm

D2-T D2 fenék/tető

389 × 337 × 18 mm

Anyag:M01; költség:C01

Szál:nincs

Nyers méret/művelet: műhelyi lezárásra.

Kontúr kész névleges méret. Vasalatfuratok gyári sablonnal.



U → ; V ↑ ; helyi (0,0) / mm

D2-BACK D2 bontható hát


389 × 384 × 8 mm

Anyag:M08; költség:C01

Szál:nincs

Nyers méret/művelet: műhelyi lezárásra.

Kontúr kész névleges méret. Vasalatfuratok gyári sablonnal.

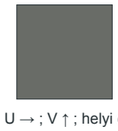

U → ; V ↑ ; helyi (0,0) / mm

D2-FRONT D2 egy magas front

422 × 378 × 18 mm

Anyag:M03; költség:C01

Szál:U vízszintes

Nyers méret/művelet: műhelyi lezárásra.

Névleges 3 mm frontköz; minimum benyomási út 2,5 mm. Korpusz elé 5 mm tervezett rés.



U → ; V ↑ ; helyi (0,0) / mm

TERVEZÉSI JAVASLAT - NEM GYÁRTÁSI JÓVÁHAGYÁS

Alkatrészlapok 17–20

D2-BOX-L D2 fiókoldal

290 × 237 × 15 mm

Anyag:M07; költség:C04

Szál:nincs

Nyers méret/művelet: műhelyi lezárásra.

Kontúr kész névleges méret. Vasalatfuratok gyári sablonnal.



U → ; V ↑ ; helyi (0,0) / mm

D2-BOX-R D2 fiókoldal

290 × 237 × 15 mm

Anyag:M07; költség:C04

Szál:nincs

Nyers méret/művelet: műhelyi lezárásra.

Kontúr kész névleges méret. Vasalatfuratok gyári sablonnal.



U → ; V ↑ ; helyi (0,0) / mm

D2-BOX-F D2 dobozelő/hát

347 × 222 × 15 mm

Anyag:M07; költség:C04

Szál:nincs

Nyers méret/művelet: műhelyi lezárásra.

Kontúr kész névleges méret. Vasalatfuratok gyári sablonnal.



U → ; V ↑ ; helyi (0,0) / mm

D2-BOX-H D2 dobozelő/hát


347 × 222 × 15 mm

Anyag:M07; költség:C04

Szál:nincs

Nyers méret/művelet: műhelyi lezárásra.

Kontúr kész névleges méret. Vasalatfuratok gyári sablonnal.

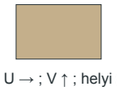

U → ; V ↑ ; helyi (0,0) / mm

TERVEZÉSI JAVASLAT - NEM GYÁRTÁSI JÓVÁHAGYÁS

Alkatrészlapok 21–24

D2-BOX-B D2 fiókfenék

347 × 290 × 15 mm

Anyag:M07; költség:C04

Szál:nincs

Nyers méret/művelet: műhelyi lezárásra.

Kontúr kész névleges méret. Vasalatfuratok gyári sablonnal.



U → ; V ↑ ; helyi (0,0) / mm

D3-L D3 korpuszoldal

337 × 420 × 18 mm

Anyag:M01; költség:C01

Szál:nincs

Nyers méret/művelet: műhelyi lezárásra.

Kontúr kész névleges méret. Vasalatfuratok gyári sablonnal.



U → ; V ↑ ; helyi (0,0) / mm

D3-R D3 korpuszoldal

337 × 420 × 18 mm

Anyag:M01; költség:C01

Szál:nincs

Nyers méret/művelet: műhelyi lezárásra.

Kontúr kész névleges méret. Vasalatfuratok gyári sablonnal.



U → ; V ↑ ; helyi (0,0) / mm

D3-B D3 fenék/tető


389 × 337 × 18 mm

Anyag:M01; költség:C01

Szál:nincs

Nyers méret/művelet: műhelyi lezárásra.

Kontúr kész névleges méret. Vasalatfuratok gyári sablonnal.

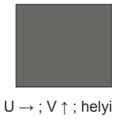

U → ; V ↑ ; helyi (0,0) / mm

TERVEZÉSI JAVASLAT - NEM GYÁRTÁSI JÓVÁHAGYÁS

Alkatrészlapok 25–28

D3-T D3 fenék/tető

389 × 337 × 18 mm

Anyag:M01; költség:C01

Szál:nincs

Nyers méret/művelet: műhelyi lezárásra.

Kontúr kész névleges méret. Vasalatfuratok gyári sablonnal.



U → ; V ↑ ; helyi (0,0) / mm

D3-BACK D3 bontható hát

389 × 384 × 8 mm

Anyag:M08; költség:C01

Szál:nincs

Nyers méret/művelet: műhelyi lezárásra.

Kontúr kész névleges méret. Vasalatfuratok gyári sablonnal.



U → ; V ↑ ; helyi (0,0) / mm

D3-FRONT D3 egy magas front

422 × 378 × 18 mm

Anyag:M03; költség:C01

Szál:U vízszintes

Nyers méret/művelet: műhelyi lezárásra.

Névleges 3 mm frontköz; minimum benyomási út 2,5 mm. Korpusz elé 5 mm tervezett rés.



U → ; V ↑ ; helyi (0,0) / mm

D3-BOX-L D3 fiókoldal


290 × 237 × 15 mm

Anyag:M07; költség:C04

Szál:nincs

Nyers méret/művelet: műhelyi lezárásra.

Kontúr kész névleges méret. Vasalatfuratok gyári sablonnal.

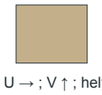

U → ; V ↑ ; helyi (0,0) / mm

TERVEZÉSI JAVASLAT - NEM GYÁRTÁSI JÓVÁHAGYÁS

Alkatrészlapok 29–32

D3-BOX-R D3 fiókoldal

290 × 237 × 15 mm

Anyag:M07; költség:C04

Szál:nincs

Nyers méret/művelet: műhelyi lezárásra.

Kontúr kész névleges méret. Vasalatfuratok gyári sablonnal.



U → ; V ↑ ; helyi (0,0) / mm

D3-BOX-F D3 dobozelő/hát

347 × 222 × 15 mm

Anyag:M07; költség:C04

Szál:nincs

Nyers méret/művelet: műhelyi lezárásra.

Kontúr kész névleges méret. Vasalatfuratok gyári sablonnal.



U → ; V ↑ ; helyi (0,0) / mm

D3-BOX-H D3 dobozelő/hát

347 × 222 × 15 mm

Anyag:M07; költség:C04

Szál:nincs

Nyers méret/művelet: műhelyi lezárásra.

Kontúr kész névleges méret. Vasalatfuratok gyári sablonnal.



U → ; V ↑ ; helyi (0,0) / mm

D3-BOX-B D3 fiókfenék


347 × 290 × 15 mm

Anyag:M07; költség:C04

Szál:nincs

Nyers méret/művelet: műhelyi lezárásra.

Kontúr kész névleges méret. Vasalatfuratok gyári sablonnal.

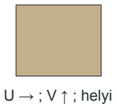

U → ; V ↑ ; helyi (0,0) / mm

TERVEZÉSI JAVASLAT - NEM GYÁRTÁSI JÓVÁHAGYÁS

Alkatrészlapok 33–36

D4-L D4 korpuszoldal

337 × 420 × 18 mm

Anyag:M01; költség:C01

Szál:nincs

Nyers méret/művelet: műhelyi lezárásra.

Kontúr kész névleges méret. Vasalatfuratok gyári sablonnal.



U → ; V ↑ ; helyi (0,0) / mm

D4-R D4 korpuszoldal

337 × 420 × 18 mm

Anyag:M01; költség:C01

Szál:nincs

Nyers méret/művelet: műhelyi lezárásra.

Kontúr kész névleges méret. Vasalatfuratok gyári sablonnal.



U → ; V ↑ ; helyi (0,0) / mm

D4-B D4 fenék/tető


994 × 337 × 18 mm

Anyag:M01; költség:C01

Szál:nincs

Nyers méret/művelet: műhelyi lezárásra.

Kontúr kész névleges méret. Vasalatfuratok gyári sablonnal.

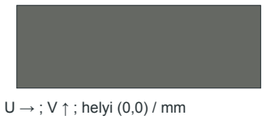

U → ; V ↑ ; helyi (0,0) / mm

D4-T D4 fenék/tető


994 × 337 × 18 mm

Anyag:M01; költség:C01

Szál:nincs

Nyers méret/művelet: műhelyi lezárásra.

Kontúr kész névleges méret. Vasalatfuratok gyári sablonnal.

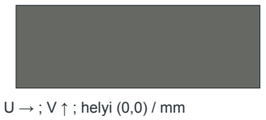

U → ; V ↑ ; helyi (0,0) / mm

TERVEZÉSI JAVASLAT - NEM GYÁRTÁSI JÓVÁHAGYÁS

Alkatrészlapok 37–40

D4-BACK D4 bontható hát

994 × 384 × 8 mm

Anyag:M08; költség:C01

Szál:nincs

Nyers méret/művelet: műhelyi lezárásra.

Kontúr kész névleges méret. Vasalatfuratok gyári sablonnal.



U → ; V ↑ ; helyi (0,0) / mm

D4-FRONT D4 egy magas front

1027 × 378 × 18 mm

Anyag:M03; költség:C01

Szál:U vízszintes

Nyers méret/művelet: műhelyi lezárásra.

Névleges 3 mm frontköz; minimum benyomási út 2,5 mm. Korpusz elé 5 mm tervezett rés.



U → ; V ↑ ; helyi (0,0) / mm

D4-BOX-L D4 fiókoldal


290 × 237 × 15 mm

Anyag:M07; költség:C04

Szál:nincs

Nyers méret/művelet: műhelyi lezárásra.

Kontúr kész névleges méret. Vasalatfuratok gyári sablonnal.

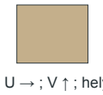

U → ; V ↑ ; helyi (0,0) / mm

D4-BOX-R D4 fiókoldal


290 × 237 × 15 mm

Anyag:M07; költség:C04

Szál:nincs

Nyers méret/művelet: műhelyi lezárásra.

Kontúr kész névleges méret. Vasalatfuratok gyári sablonnal.

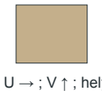

U → ; V ↑ ; helyi (0,0) / mm

TERVEZÉSI JAVASLAT - NEM GYÁRTÁSI JÓVÁHAGYÁS

Alkatrészlapok 41–44

D4-BOX-F D4 dobozelő/hát

952 × 222 × 15 mm

Anyag:M07; költség:C04

Szál:nincs

Nyers méret/művelet: műhelyi lezárásra.

Kontúr kész névleges méret. Vasalatfuratok gyári sablonnal.



U → ; V ↑ ; helyi (0,0) / mm

D4-BOX-H D4 dobozelő/hát

952 × 222 × 15 mm

Anyag:M07; költség:C04

Szál:nincs

Nyers méret/művelet: műhelyi lezárásra.

Kontúr kész névleges méret. Vasalatfuratok gyári sablonnal.



U → ; V ↑ ; helyi (0,0) / mm

D4-BOX-B D4 fiókfenék

952 × 290 × 15 mm

Anyag:M07; költség:C04

Szál:nincs

Nyers méret/művelet: műhelyi lezárásra.

Kontúr kész névleges méret. Vasalatfuratok gyári sablonnal.



U → ; V ↑ ; helyi (0,0) / mm

D5-L D5 korpuszoldal

337 × 420 × 18 mm

Anyag:M01; költség:C01

Szál:nincs

Nyers méret/művelet: műhelyi lezárásra.

Kontúr kész névleges méret. Vasalatfuratok gyári sablonnal.



U → ; V ↑ ; helyi (0,0) / mm

TERVEZÉSI JAVASLAT - NEM GYÁRTÁSI JÓVÁHAGYÁS

Alkatrészlapok 45–48

D5-R D5 korpuszoldal

337 × 420 × 18 mm

Anyag:M01; költség:C01

Szál:nincs

Nyers méret/művelet: műhelyi lezárásra.

Kontúr kész névleges méret. Vasalatfuratok gyári sablonnal.



U → ; V ↑ ; helyi (0,0) / mm

D5-B D5 fenék/tető

389 × 337 × 18 mm

Anyag:M01; költség:C01

Szál:nincs

Nyers méret/művelet: műhelyi lezárásra.

Kontúr kész névleges méret. Vasalatfuratok gyári sablonnal.



U → ; V ↑ ; helyi (0,0) / mm

D5-T D5 fenék/tető

389 × 337 × 18 mm

Anyag:M01; költség:C01

Szál:nincs

Nyers méret/művelet: műhelyi lezárásra.

Kontúr kész névleges méret. Vasalatfuratok gyári sablonnal.



U → ; V ↑ ; helyi (0,0) / mm

D5-BACK D5 bontható hát


389 × 384 × 8 mm

Anyag:M08; költség:C01

Szál:nincs

Nyers méret/művelet: műhelyi lezárásra.

Kontúr kész névleges méret. Vasalatfuratok gyári sablonnal.

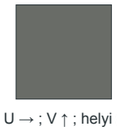

U → ; V ↑ ; helyi (0,0) / mm

TERVEZÉSI JAVASLAT - NEM GYÁRTÁSI JÓVÁHAGYÁS

Alkatrészlapok 49–52

D5-FRONT D5 egy magas front

422 × 378 × 18 mm

Anyag:M03; költség:C01

Szál:U vízszintes

Nyers méret/művelet: műhelyi lezárásra.

Névleges 3 mm frontköz; minimum benyomási út 2,5 mm. Korpusz elé 5 mm tervezett rés.



U → ; V ↑ ; helyi (0,0) / mm

D5-BOX-L D5 fiókoldal

290 × 237 × 15 mm

Anyag:M07; költség:C04

Szál:nincs

Nyers méret/művelet: műhelyi lezárásra.

Kontúr kész névleges méret. Vasalatfuratok gyári sablonnal.



U → ; V ↑ ; helyi (0,0) / mm

D5-BOX-R D5 fiókoldal


290 × 237 × 15 mm

Anyag:M07; költség:C04

Szál:nincs

Nyers méret/művelet: műhelyi lezárásra.

Kontúr kész névleges méret. Vasalatfuratok gyári sablonnal.

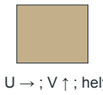

U → ; V ↑ ; helyi (0,0) / mm

D5-BOX-F D5 dobozelő/hát


347 × 222 × 15 mm

Anyag:M07; költség:C04

Szál:nincs

Nyers méret/művelet: műhelyi lezárásra.

Kontúr kész névleges méret. Vasalatfuratok gyári sablonnal.

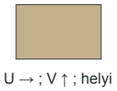

U → ; V ↑ ; helyi (0,0) / mm

TERVEZÉSI JAVASLAT - NEM GYÁRTÁSI JÓVÁHAGYÁS

Alkatrészlapok 53–56

D5-BOX-H D5 dobozelő/hát

347 × 222 × 15 mm

Anyag:M07; költség:C04

Szál:nincs

Nyers méret/művelet: műhelyi lezárásra.

Kontúr kész névleges méret. Vasalatfuratok gyári sablonnal.



U → ; V ↑ ; helyi (0,0) / mm

D5-BOX-B D5 fiókfenék

347 × 290 × 15 mm

Anyag:M07; költség:C04

Szál:nincs

Nyers méret/művelet: műhelyi lezárásra.

Kontúr kész névleges méret. Vasalatfuratok gyári sablonnal.



U → ; V ↑ ; helyi (0,0) / mm

D6-L D6 korpuszoldal


337 × 420 × 18 mm

Anyag:M01; költség:C01

Szál:nincs

Nyers méret/művelet: műhelyi lezárásra.

Kontúr kész névleges méret. Vasalatfuratok gyári sablonnal.

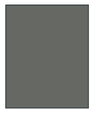

U → ; V ↑ ; helyi (0,0) / mm

D6-R D6 korpuszoldal

337 × 260 × 18 mm

Anyag:M01; költség:C01

Szál:nincs

Nyers méret/művelet: műhelyi lezárásra.

Kontúr kész névleges méret. Vasalatfuratok gyári sablonnal.



U → ; V ↑ ; helyi (0,0) / mm

TERVEZÉSI JAVASLAT - NEM GYÁRTÁSI JÓVÁHAGYÁS

Alkatrészlapok 57–60

D6-B D6 fenék/tető

327 × 337 × 18 mm

Anyag:M01; költség:C01

Szál:nincs

Nyers méret/művelet: műhelyi lezárásra.

Kontúr kész névleges méret. Vasalatfuratok gyári sablonnal.



U → ; V ↑ ; helyi (0,0) / mm

D6-T D6 fenék/tető

327 × 337 × 18 mm

Anyag:M01; költség:C01

Szál:nincs

Nyers méret/művelet: műhelyi lezárásra.

Kontúr kész névleges méret. Vasalatfuratok gyári sablonnal.



U → ; V ↑ ; helyi (0,0) / mm

D6-BACK D6 bontható hát

389 × 384 × 8 mm

Anyag:M08; költség:C01

Szál:nincs

Nyers méret/művelet: műhelyi lezárásra.

Kontúr kész névleges méret. Vasalatfuratok gyári sablonnal.



U → ; V ↑ ; helyi (0,0) / mm

D6-FRONT D6 egy magas front

402.5 × 378 × 18 mm

Anyag:M03; költség:C01

Szál:U vízszintes

Nyers méret/művelet: műhelyi lezárásra.

Névleges 3 mm frontköz; minimum benyomási út 2,5 mm. Korpusz elé 5 mm tervezett rés.



U → ; V ↑ ; helyi (0,0) / mm

TERVEZÉSI JAVASLAT - NEM GYÁRTÁSI JÓVÁHAGYÁS

Alkatrészlapok 61–64

D6-BOX-L D6 fiókoldal

290 × 237 × 15 mm

Anyag:M07; költség:C04

Szál:nincs

Nyers méret/művelet: műhelyi lezárásra.

Kontúr kész névleges méret. Vasalatfuratok gyári sablonnal.



U → ; V ↑ ; helyi (0,0) / mm

D6-BOX-R D6 fiókoldal

290 × 237 × 15 mm

Anyag:M07; költség:C04

Szál:nincs

Nyers méret/művelet: műhelyi lezárásra.

Kontúr kész névleges méret. Vasalatfuratok gyári sablonnal.



U → ; V ↑ ; helyi (0,0) / mm

D6-BOX-F D6 dobozelő/hát

347 × 222 × 15 mm

Anyag:M07; költség:C04

Szál:nincs

Nyers méret/művelet: műhelyi lezárásra.

Kontúr kész névleges méret. Vasalatfuratok gyári sablonnal.



U → ; V ↑ ; helyi (0,0) / mm

D6-BOX-H D6 dobozelő/hát


347 × 222 × 15 mm

Anyag:M07; költség:C04

Szál:nincs

Nyers méret/művelet: műhelyi lezárásra.

Kontúr kész névleges méret. Vasalatfuratok gyári sablonnal.

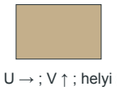

U → ; V ↑ ; helyi (0,0) / mm

TERVEZÉSI JAVASLAT - NEM GYÁRTÁSI JÓVÁHAGYÁS

Alkatrészlapok 65–68

D6-BOX-B D6 fiókfenék

347 × 290 × 15 mm

Anyag:M07; költség:C04

Szál:nincs

Nyers méret/művelet: műhelyi lezárásra.

Kontúr kész névleges méret. Vasalatfuratok gyári sablonnal.



U → ; V ↑ ; helyi (0,0) / mm

T-L Torony oldallap

337 × 2525 × 18 mm

Anyag:M01; költség:U03

Szál:nincs

Nyers méret/művelet: műhelyi lezárásra.

Kontúr kész névleges méret. Vasalatfuratok gyári sablonnal.



U → ; V ↑ ; helyi (0,0) / mm

T-R Torony oldallap

337 × 2205 × 18 mm

Anyag:M01; költség:U03

Szál:nincs

Nyers méret/művelet: műhelyi lezárásra.

Kontúr kész névleges méret. Vasalatfuratok gyári sablonnal.



U → ; V ↑ ; helyi (0,0) / mm

T-B Torony fenék/tető

834 × 337 × 18 mm

Anyag:M01; költség:U03

Szál:nincs

Nyers méret/művelet: műhelyi lezárásra.

Kontúr kész névleges méret. Vasalatfuratok gyári sablonnal.



U → ; V ↑ ; helyi (0,0) / mm

TERVEZÉSI JAVASLAT - NEM GYÁRTÁSI JÓVÁHAGYÁS

Alkatrészlapok 69–72

T-C Torony középosztó

337 × 2269 × 18 mm

Anyag:M01; költség:U03

Szál:nincs

Nyers méret/művelet: műhelyi lezárásra.

Kontúr kész névleges méret. Vasalatfuratok gyári sablonnal.



U → ; V ↑ ; helyi (0,0) / mm

T-L-S1 Állítható polc

406 × 290 × 18 mm

Anyag:M01; költség:U03

Szál:nincs

Nyers méret/művelet: műhelyi lezárásra.

1 mm oldalhézag; hasznos polcméret 406×290.
Elülső35mm szabad sáv a fényprofilnak. Terhelést műhely igazolja.



U → ; V ↑ ; helyi (0,0) / mm

T-L-S2 Állítható polc


406 × 290 × 18 mm

Anyag:M01; költség:U03

Szál:nincs

Nyers méret/művelet: műhelyi lezárásra.

1 mm oldalhézag; hasznos polcméret 406×290.
Elülső35mm szabad sáv a fényprofilnak. Terhelést műhely igazolja.

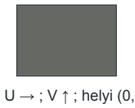

U → ; V ↑ ; helyi (0,0) / mm

T-L-S3 Állítható polc


406 × 290 × 18 mm

Anyag:M01; költség:U03

Szál:nincs

Nyers méret/művelet: műhelyi lezárásra.

1 mm oldalhézag; hasznos polcméret 406×290.
Elülső35mm szabad sáv a fényprofilnak. Terhelést műhely igazolja.

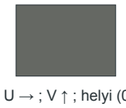

U → ; V ↑ ; helyi (0,0) / mm

TERVEZÉSI JAVASLAT - NEM GYÁRTÁSI JÓVÁHAGYÁS

Alkatrészlapok 73–76

T-L-S4 Állítható polc

406 × 290 × 18 mm

Anyag:M01; költség:U03

Szál:nincs

Nyers méret/művelet: műhelyi lezárásra.

1 mm oldalhézag; hasznos polcméret 406×290.
Elülső35mm szabad sáv a fényprofilnak. Terhelést műhely igazolja.



U → ; V ↑ ; helyi (0,0) / mm

T-L-S5 Állítható polc

406 × 290 × 18 mm

Anyag:M01; költség:U03

Szál:nincs

Nyers méret/művelet: műhelyi lezárásra.

1 mm oldalhézag; hasznos polcméret 406×290.
Elülső35mm szabad sáv a fényprofilnak. Terhelést műhely igazolja.



U → ; V ↑ ; helyi (0,0) / mm

T-L-BACK Bontható felső hát

406 × 1921 × 8 mm

Anyag:M08; költség:U03

Szál:nincs

Nyers méret/művelet: műhelyi lezárásra.

Kontúr kész névleges méret. Vasalatfuratok gyári sablonnal.



U → ; V ↑ ; helyi (0,0) / mm

T-L-SERVICE Bontható alsó szervizfedél

406 × 345 × 8 mm

Anyag:M08; költség:U03

Szál:nincs

Nyers méret/művelet: műhelyi lezárásra.

Előlről csavarozva kiemelhető; alsó rekeszben 240 mm tárolási mélység.



U → ; V ↑ ; helyi (0,0) / mm

TERVEZÉSI JAVASLAT - NEM GYÁRTÁSI JÓVÁHAGYÁS

Alkatrészlapok 77–80

T-R-S1 Állítható polc

406 × 290 × 18 mm

Anyag:M01; költség:U03

Szál:nincs

Nyers méret/művelet: műhelyi lezárásra.

1 mm oldalhézag; hasznos polcméret 406×290.
Elülső35mm szabad sáv a fényprofilnak. Terhelést műhely igazolja.



U → ; V ↑ ; helyi (0,0) / mm

T-R-S2 Állítható polc

406 × 290 × 18 mm

Anyag:M01; költség:U03

Szál:nincs

Nyers méret/művelet: műhelyi lezárásra.

1 mm oldalhézag; hasznos polcméret 406×290.
Elülső35mm szabad sáv a fényprofilnak. Terhelést műhely igazolja.



U → ; V ↑ ; helyi (0,0) / mm

T-R-S3 Állítható polc

406 × 290 × 18 mm

Anyag:M01; költség:U03

Szál:nincs

Nyers méret/művelet: műhelyi lezárásra.

1 mm oldalhézag; hasznos polcméret 406×290.
Elülső35mm szabad sáv a fényprofilnak. Terhelést műhely igazolja.



U → ; V ↑ ; helyi (0,0) / mm

T-R-S4 Állítható polc

406 × 290 × 18 mm

Anyag:M01; költség:U03

Szál:nincs

Nyers méret/művelet: műhelyi lezárásra.

1 mm oldalhézag; hasznos polcméret 406×290.
Elülső35mm szabad sáv a fényprofilnak. Terhelést műhely igazolja.



U → ; V ↑ ; helyi (0,0) / mm

TERVEZÉSI JAVASLAT - NEM GYÁRTÁSI JÓVÁHAGYÁS

Alkatrészlapok 81–84

T-R-S5 Állítható polc

406 × 290 × 18 mm

Anyag:M01; költség:U03

Szál:nincs

Nyers méret/művelet: műhelyi lezárásra.

1 mm oldalhézag; hasznos polcméret 406×290.
Elülső35mm szabad sáv a fényprofilnak. Terhelést műhely igazolja.



U → ; V ↑ ; helyi (0,0) / mm

T-R-BACK Bontható felső hát

406 × 1921 × 8 mm

Anyag:M08; költség:U03

Szál:nincs

Nyers méret/művelet: műhelyi lezárásra.

Kontúr kész névleges méret. Vasalatfuratok gyári sablonnal.



U → ; V ↑ ; helyi (0,0) / mm

T-R-SERVICE Bontható alsó szervizfedél

406 × 345 × 8 mm

Anyag:M08; költség:U03

Szál:nincs

Nyers méret/művelet: műhelyi lezárásra.

Előlről csavarozva kiemelhető; alsó rekeszben 240 mm tárolási mélység.



U → ; V ↑ ; helyi (0,0) / mm

T-DOOR-L Torony ajtó

412.5 × 2683 × 18 mm

Anyag:M03; költség:U04

Szál:V függőleges

Nyers méret/művelet: műhelyi lezárásra.

Rugó nélküli inset CLIP top + mágneses TIP-ON.
Bal6/jobb5 pánt előirányzat, tömeg és ráütés alapján véglegesítendő; csillapítás nincs. A teljes peremfény az ajtóval mozog. Pántoldali24V hajlításálló vezeték, oldható csatlakozó és húzásmentesítés; teljes nyitásnál vezetékpróba.



U → ; V ↑ ; helyi (0,0) / mm

TERVEZÉSI JAVASLAT - NEM GYÁRTÁSI JÓVÁHAGYÁS

Alkatrészlapok 85–88

T-DOOR-R Torony ajtó

412.5 × 2281 × 18 mm

Anyag:M03; költség:U04

Szál:V függőleges

Nyers méret/művelet: műhelyi lezárásra.

Rugó nélküli inset CLIP top + mágneses TIP-ON. Bal6/jobb5 pánt előirányzat, tömeg és ráütés alapján véglegesítendő; csillapítás nincs.



U → ; V ↑ ; helyi (0,0) / mm

TEXTILE Elefántcsont szövetbetét

360 × 2515 × 8 mm

Anyag:M05; költség:U07

Szál:nincs

Nyers méret/művelet: műhelyi lezárásra.

R60 cserélhető szövetbetét; tulajdonosi kép szerinti lágyabb ív javaslat.



U → ; V ↑ ; helyi (0,0) / mm

BG-1 Bontható szürke háttérpanel

678 × 2305 × 18 mm

Anyag:M04; költség:U01

Szál:V függőleges

Nyers méret/művelet: műhelyi lezárásra.

3 mm valós függőleges hézag. 20 mm felfelé emelést nem igénylő előre oldható kapocs. Panelt TV levétele után lehet bontani.



U → ; V ↑ ; helyi (0,0) / mm

BG-2 Bontható szürke háttérpanel

679.5 × 2305 × 18 mm

Anyag:M04; költség:U01

Szál:V függőleges

Nyers méret/művelet: műhelyi lezárásra.

3 mm valós függőleges hézag. 20 mm felfelé emelést nem igénylő előre oldható kapocs. Panelt TV levétele után lehet bontani.



U → ; V ↑ ; helyi (0,0) / mm

TERVEZÉSI JAVASLAT - NEM GYÁRTÁSI JÓVÁHAGYÁS

Alkatrészlapok 89–92

BG-3 Bontható szürke háttérpanel

679.5 × 2305 × 18 mm

Anyag:M04; költség:U01

Szál:V függőleges

Nyers méret/művelet: műhelyi lezárásra.

3 mm valós függőleges hézag. 20 mm felfelé emelést nem igénylő előre oldható kapocs. Panelt TV levétele után lehet bontani.



U → ; V ↑ ; helyi (0,0) / mm

BG-4 Bontható szürke háttérpanel

678 × 2305 × 18 mm

Anyag:M04; költség:U01

Szál:V függőleges

Nyers méret/művelet: műhelyi lezárásra.

3 mm valós függőleges hézag. 20 mm felfelé emelést nem igénylő előre oldható kapocs. Panelt TV levétele után lehet bontani.



U → ; V ↑ ; helyi (0,0) / mm

BATTEN-1 Háttér falsín

40 × 2235 × 40 mm

Anyag:M01; költség:F02

Szál:nincs

Nyers méret/művelet: műhelyi lezárásra.

Falméret és horgony méretezés után rögzíthető. 20 mm előrefelé oldható kapocstér y40..60.



U → ; V ↑ ; helyi (0,0) / mm

BATTEN-2 Háttér falsín

40 × 2235 × 40 mm

Anyag:M01; költség:F02

Szál:nincs

Nyers méret/művelet: műhelyi lezárásra.

Falméret és horgony méretezés után rögzíthető. 20 mm előrefelé oldható kapocstér y40..60.



U → ; V ↑ ; helyi (0,0) / mm

TERVEZÉSI JAVASLAT - NEM GYÁRTÁSI JÓVÁHAGYÁS

Alkatrészlapok 93–96

BATTEN-3 Háttér falsín

40 × 2235 × 40 mm

Anyag:M01; költség:F02

Szál:nincs

Nyers méret/művelet: műhelyi lezárásra.

Falméret és horgony méretezés után rögzíthető. 20 mm előrefelé oldható kapocstér y40..60.

U → ; V ↑ ; helyi (0,0) / mm

BATTEN-4 Háttér falsín

40 × 2235 × 40 mm

Anyag:M01; költség:F02

Szál:nincs

Nyers méret/művelet: műhelyi lezárásra.

Falméret és horgony méretezés után rögzíthető. 20 mm előrefelé oldható kapocstér y40..60.

U → ; V ↑ ; helyi (0,0) / mm

BATTEN-5 Háttér falsín

40 × 2235 × 40 mm

Anyag:M01; költség:F02

Szál:nincs

Nyers méret/művelet: műhelyi lezárásra.

Falméret és horgony méretezés után rögzíthető. 20 mm előrefelé oldható kapocstér y40..60.



U → ; V ↑ ; helyi (0,0) / mm

CURVE-T-TOP R100 rétegelt, íves toronysapka

870 × 100 × 337 mm BEFOGLALÓ; héj18mm

Anyag:M02; költség:U05

Szál:nincs

Nyers méret/művelet: műhelyi lezárásra.

18 mm rétegvastagságú hajlított/lamellázott héj, 337mm mélységben. Nem 337mm vastag MDF lap! R100 külső/R82 belső, műhelysablon és rétegrend jóváhagyása kell.



U → ; V ↑ ; helyi (0,0) / mm

TERVEZÉSI JAVASLAT - NEM GYÁRTÁSI JÓVÁHAGYÁS

Alkatrészlapok 97–100

FRAME-T-TOP R100 frontkeret záróelem

870 × 100 × 18 mm

Anyag:M02; költség:U05

Szál:nincs

Nyers méret/művelet: műhelyi lezárásra.

Kontúr kész névleges méret. Vasalatfuratok gyári sablonnal.



U → ; V ↑ ; helyi (0,0) / mm

CURVE-T-BOT R100 rétegelt, íves toronysapka

870 × 100 × 337 mm BEFOGLALÓ; héj18mm

Anyag:M02; költség:U05

Szál:nincs

Nyers méret/művelet: műhelyi lezárásra.

18 mm rétegvastagságú hajlított/lamellázott héj, 337mm mélységben. Nem 337mm vastag MDF lap! R100 külső/R82 belső, műhelysablon és rétegrend jóváhagyása kell.



U → ; V ↑ ; helyi (0,0) / mm

FRAME-T-BOT R100 frontkeret záróelem


870 × 100 × 18 mm

Anyag:M02; költség:U05

Szál:nincs

Nyers méret/művelet: műhelyi lezárásra.

Kontúr kész névleges méret. Vasalatfuratok gyári sablonnal.

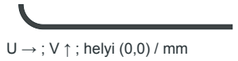

U → ; V ↑ ; helyi (0,0) / mm

FRAME-T-L Torony fix függőleges keret

18 × 2525 × 18 mm

Anyag:M02; költség:U05

Szál:nincs

Nyers méret/művelet: műhelyi lezárásra.

Kontúr kész névleges méret. Vasalatfuratok gyári sablonnal.



U → ; V ↑ ; helyi (0,0) / mm

TERVEZÉSI JAVASLAT - NEM GYÁRTÁSI JÓVÁHAGYÁS

Alkatrészlapok 101–104

FRAME-T-R Torony fix függőleges keret

18 × 2205 × 18 mm

Anyag:M02; költség:U05

Szál:nincs

Nyers méret/művelet: műhelyi lezárásra.

Kontúr kész névleges méret. Vasalatfuratok gyári sablonnal.



U → ; V ↑ ; helyi (0,0) / mm

FRAME-T-MID Torony fiók feletti fix osztó

433.5 × 18 × 18 mm

Anyag:M02; költség:U05

Szál:nincs

Nyers méret/művelet: műhelyi lezárásra.

Kontúr kész névleges méret. Vasalatfuratok gyári sablonnal.

U → ; V ↑ ; helyi (0,0) / mm

FRAME-B-LOW-1 Alsó fix keret, jobb végén R80

850 × 18 × 18 mm

Anyag:M02; költség:U05

Szál:nincs

Nyers méret/művelet: műhelyi lezárásra.

Kontúr kész névleges méret. Vasalatfuratok gyári sablonnal.

U → ; V ↑ ; helyi (0,0) / mm

FRAME-B-LOW-2 Alsó fix keret, jobb végén R80

1030 × 18 × 18 mm

Anyag:M02; költség:U05

Szál:nincs

Nyers méret/művelet: műhelyi lezárásra.

Kontúr kész névleges méret. Vasalatfuratok gyári sablonnal.

U → ; V ↑ ; helyi (0,0) / mm

TERVEZÉSI JAVASLAT - NEM GYÁRTÁSI JÓVÁHAGYÁS

Alkatrészlapok 105–108

FRAME-B-LOW-3 Alsó fix keret, jobb végén R80

770 × 18 × 18 mm

Anyag:M02; költség:U05

Szál:nincs

Nyers méret/művelet: műhelyi lezárásra.

Kontúr kész névleges méret. Vasalatfuratok gyári sablonnal.

U → ; V ↑ ; helyi (0,0) / mm

FRAME-B-HIGH-1 Alsó fix keret, jobb végén R80

850 × 18 × 18 mm

Anyag:M02; költség:U05

Szál:nincs

Nyers méret/művelet: műhelyi lezárásra.

Kontúr kész névleges méret. Vasalatfuratok gyári sablonnal.

U → ; V ↑ ; helyi (0,0) / mm

FRAME-B-HIGH-2 Alsó fix keret, jobb végén R80

1030 × 18 × 18 mm

Anyag:M02; költség:U05

Szál:nincs

Nyers méret/művelet: műhelyi lezárásra.

Kontúr kész névleges méret. Vasalatfuratok gyári sablonnal.

U → ; V ↑ ; helyi (0,0) / mm

FRAME-B-HIGH-3 Alsó fix keret, jobb végén R80

770 × 18 × 18 mm

Anyag:M02; költség:U05

Szál:nincs

Nyers méret/művelet: műhelyi lezárásra.

Kontúr kész névleges méret. Vasalatfuratok gyári sablonnal.

U → ; V ↑ ; helyi (0,0) / mm

TERVEZÉSI JAVASLAT - NEM GYÁRTÁSI JÓVÁHAGYÁS

Alkatrészlapok 109–112

FRAME-B-TOP R80 alsó jobb sarok

80 × 80 × 18 mm

Anyag:M02; költség:U05

Szál:nincs

Nyers méret/művelet: műhelyi lezárásra.

Kontúr kész névleges méret. Vasalatfuratok gyári sablonnal.

U → ; V ↑ ; helyi (0,0) / mm

CURVE-B-TOP R80 laminált alsó jobb sarok

80 × 80 × 337 mm BEFOGLALÓ; héj18mm

Anyag:M02; költség:U05

Szál:nincs

Nyers méret/művelet: műhelyi lezárásra.

18mm rétegvastagságú íves héj,337mm mély. Nem tömörlap. Pontos rétegrend és ragasztósablon műhelyi feladat.

U → ; V ↑ ; helyi (0,0) / mm

FRAME-B-BOT R80 alsó jobb sarok

80 × 80 × 18 mm

Anyag:M02; költség:U05

Szál:nincs

Nyers méret/művelet: műhelyi lezárásra.

Kontúr kész névleges méret. Vasalatfuratok gyári sablonnal.



U → ; V ↑ ; helyi (0,0) / mm

CURVE-B-BOT R80 laminált alsó jobb sarok

80 × 80 × 337 mm BEFOGLALÓ; héj18mm

Anyag:M02; költség:U05

Szál:nincs

Nyers méret/művelet: műhelyi lezárásra.

18mm rétegvastagságú íves héj,337mm mély. Nem tömörlap. Pontos rétegrend és ragasztósablon műhelyi feladat.



U → ; V ↑ ; helyi (0,0) / mm

TERVEZÉSI JAVASLAT - NEM GYÁRTÁSI JÓVÁHAGYÁS

Alkatrészlapok 113–116

FRAME-B-R Alsó jobb fix keret

18 × 260 × 18 mm

Anyag:M02; költség:U05

Szál:nincs

Nyers méret/művelet: műhelyi lezárásra.

Kontúr kész névleges méret. Vasalatfuratok gyári sablonnal.

U → ; V ↑ ; helyi (0,0) / mm

TV-LINK Folytonos íves TV-réteg LINK


628.5 × 1580 × 18 mm

Anyag:M03; költség:U06

Szál:V függőleges

Nyers méret/művelet: műhelyi lezárásra.

A kontúr a toronyhoz csatlakozik és az alsó fedlapig fut. Nem külön lebegő téglalap. R160 homorú felkanyarodás/R140 felső átfordulás/R100 jobb sarok.3mm panelhézag; bal csatlakozás takart szerelési hézaga a torony mögött.

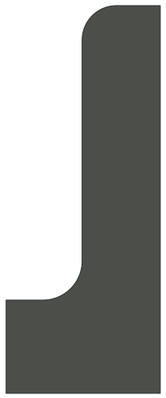

U → ; V ↑ ; helyi (0,0) / mm

TV-MID Folytonos íves TV-réteg MID

1047 × 1580 × 18 mm

Anyag:M03; költség:U06

Szál:V függőleges

Nyers méret/művelet: műhelyi lezárásra.

A kontúr a toronyhoz csatlakozik és az alsó fedlapig fut. Nem külön lebegő téglalap. R160 homorú felkanyarodás/R140 felső átfordulás/R100 jobb sarok.3mm panelhézag; bal csatlakozás takart szerelési hézaga a torony mögött.



U → ; V ↑ ; helyi (0,0) / mm

TV-END Folytonos íves TV-réteg END

948.5 × 1580 × 18 mm

Anyag:M03; költség:U06

Szál:V függőleges

Nyers méret/művelet: műhelyi lezárásra.

A kontúr a toronyhoz csatlakozik és az alsó fedlapig fut. Nem külön lebegő téglalap. R160 homorú felkanyarodás/R140 felső átfordulás/R100 jobb sarok.3mm panelhézag; bal csatlakozás takart szerelési hézaga a torony mögött.



U → ; V ↑ ; helyi (0,0) / mm

TERVEZÉSI JAVASLAT - NEM GYÁRTÁSI JÓVÁHAGYÁS

Alkatrészlapok 117–120

TV-SPACER-1 TV réteg távtartó

2530 × 30 × 17 mm

Anyag:M02; költség:U06

Szál:nincs

Nyers méret/művelet: műhelyi lezárásra.

Felső sín csak a panel által takart részen: LINK bal felső kivágásánál helyszíni rövidítés!

U → ; V ↑ ; helyi (0,0) / mm

TV-SPACER-2 TV réteg távtartó

2020 × 30 × 17 mm

Anyag:M02; költség:U06

Szál:nincs

Nyers méret/művelet: műhelyi lezárásra.

Felső sín csak a panel által takart részen: LINK bal felső kivágásánál helyszíni rövidítés!

U → ; V ↑ ; helyi (0,0) / mm

T-LOW-DIV Bal alsó rekesz jobb oldala


337 × 402 × 18 mm

Anyag:M01; költség:U03

Szál:nincs

Nyers méret/művelet: műhelyi lezárásra.

Kontúr kész névleges méret. Vasalatfuratok gyári sablonnal.

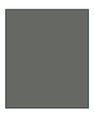

U → ; V ↑ ; helyi (0,0) / mm

T-LOW-BACK Bal alsó rekesz bontható háta

399 × 402 × 8 mm

Anyag:M08; költség:U03

Szál:nincs

Nyers méret/művelet: műhelyi lezárásra.

A teljes magas bal ajtó mögött; nincs fiók. Alsó bal R82 illesztés.



U → ; V ↑ ; helyi (0,0) / mm

TERVEZÉSI JAVASLAT - NEM GYÁRTÁSI JÓVÁHAGYÁS