
WSG A-902 / KYOTO INK

Médiafal | színes homlokzat, frontosztás és grafika

R11 • R10 külső geometriából továbbvezetett ajánlati terv • minden méret mm • helyszínen nem felmért

A–A ELÖLNÉZET 1:10

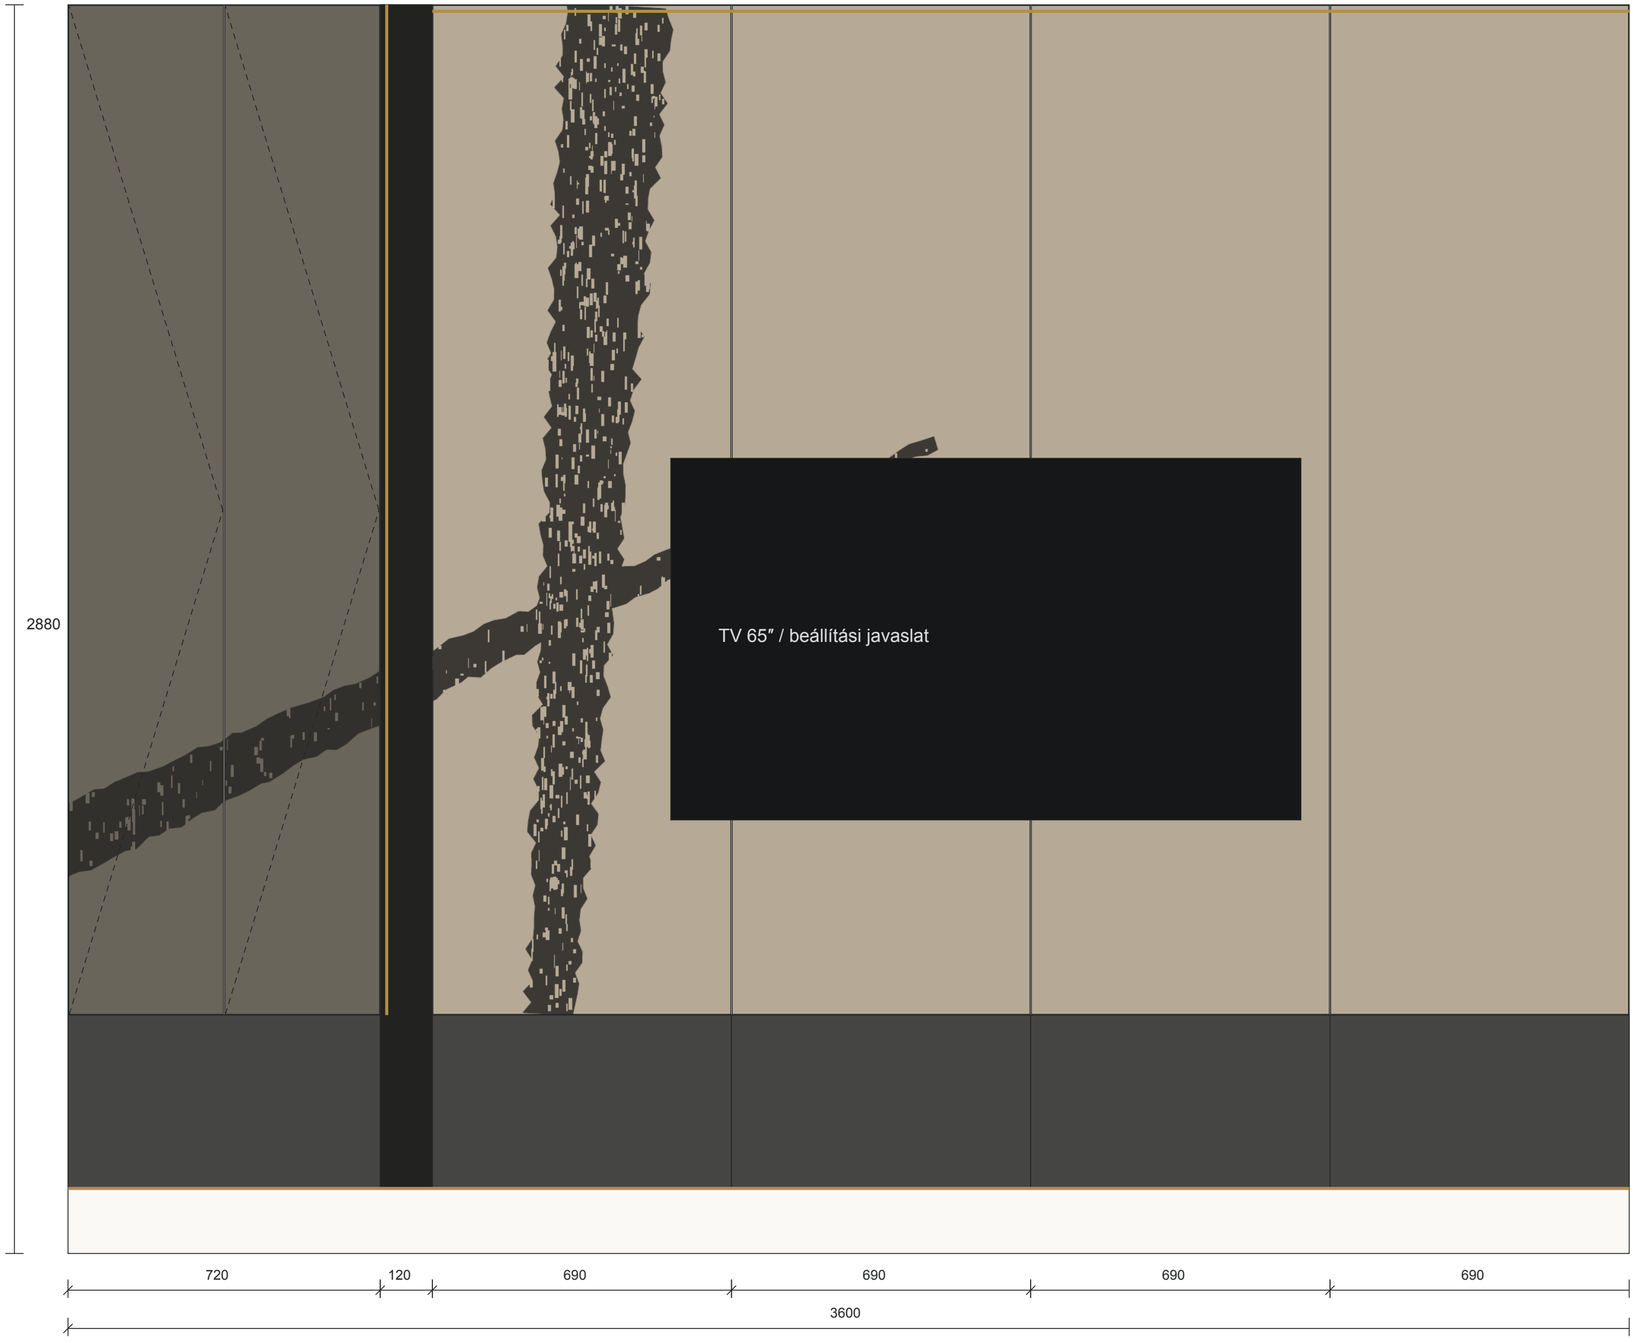

01 LÁTVÁNY

A torony, a 120-as visszahúzás és a négy panelmező együtt3600. A világos felület nem kő: nyomtatott hordozó. A színek tájékoztatóak; mintával véglegesítendők.

02 FRONTOK

Torony2×357×2327; alsó1×717×397 +4×687×397. Névleges modulonként3mm hézag. Pántolás és ajtóvetemedés gyártói ellenőrzéssel.

03 GRAFIKA

R06 INK-W01_mask.png képi munkaforrás. R11-en folytonos koordinátával szemléltetve. Gyártási felbontás, vágójel, kifutó és ajtórés külön nyomdai jóváhagyás.

04 TV

1453×834mm befoglaló; a rajzi1000mm alsó él beállítási javaslat, nem az R10 képből felmért adat. A konzolhelyet ülőszemmagasság és gyári VESA alapján véglegesíteni kell.

05 KÖLTSÉGKÓD

KI-030:765500Ft; KI-031:350000Ft; KI-032:135000Ft. Összes1250500Ft becsült asztalos keret. Fény külön KI-114150000Ft. Új ajánlattal igazolandó.

M01 grafit jelölt

M02 nyomathordozó

M03 belső világos lap

AJÁNLATKÉRÉSRE / FELMÉRÉSRE VÁR — NEM GYÁRTÁSI KIADÁS

Méretforrás: R10 + geometry_lock_A902_v2b; belsők R11 tervezési javaslat. Nyomat/minta nem jóváhagyott.


2026.10.28. | 1:10 / részletek jelölve

KI-R11 | N-01 | A2 fekvő, 100%-os nyomtatás

WSG A-902 / KYOTO INK

Médiafal | belső nézet, rekeszek és tárolókapacitás

R11 • R10 külső geometriából továbbvezetett ajánlati terv • minden méret mm • helyszínen nem felmért

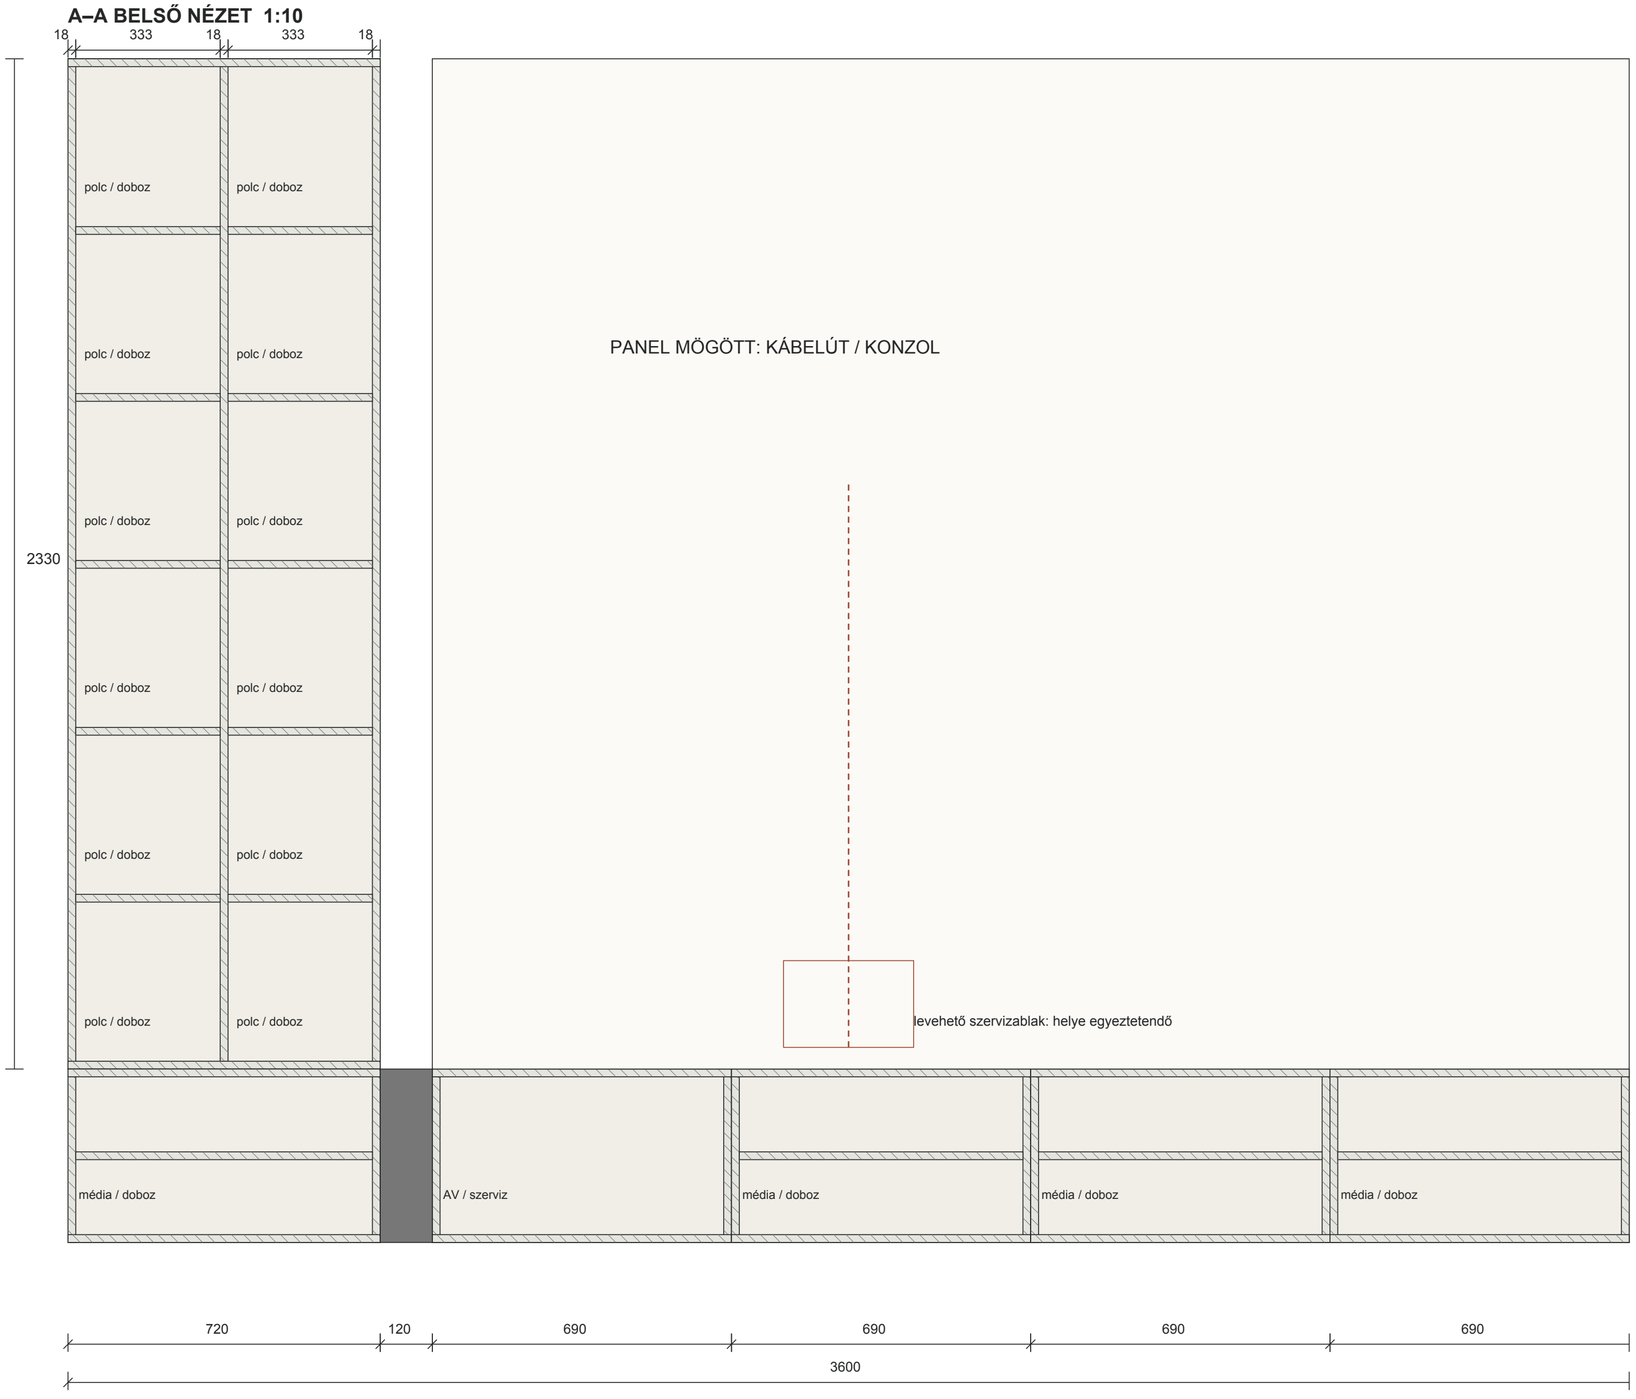

T-01 / TORONY

2 rekesz,333mm elméleti tiszta szélesség;5-5 állítható polc. Polcméret331×320×18mm (2mm szerelési játék). A polcok10db,3,31folyóméter és1,059m² polcfelület; a fenéklap nincs beleszámolva.

A-01 / ALSÓ

5 önálló modul.1×684 és4×654mm tiszta szélesség. Első és utolsó3 modulban1-1 polc; az ablak felőli második helyett a840mm-nél kezdődő modul AV-szervizrekesz, polc nélkül.

HASZNÁLAT

Torony: könyvek, társasjáték, zárt tárolódoboz. Alsó: médiaeszköz és kábel, játékdoboz, távirányító. Tápegység mellett sem textil, sem papír nem tárolható.

NYITÁS

Torony kifelé nyíló két front. Alsó oldalra nyíló csillapított frontjavaslat. Ajtónyitás a kanapéval külön használati próbát igényel; nincs teljes használati PASS.

STÁTUSZ

Ezek R11 tényleges belső kiosztási javaslatok, még nem szerepelnek részletes alkatrészként az R10 Blender-modellben. A render nem mutatja a belsőt.

AJÁNLATKÉRÉSRE / FELMÉRÉSRE VÁR — NEM GYÁRTÁSI KIADÁS

Méretforrás: R10 + geometry_lock_A902_v2b; belsők R11 tervezési javaslat. Nyomat/minta nem jóváhagyott.

2026.10.28. | 1:10 / részletek jelölve


KI-R11 | N-02 | A2 fekvő, 100%-os nyomtatás

WSG A-902 / KYOTO INK

Médiafal | alaprajz, oldalnézet és nyitási hely

R11 • R10 külső geometriából továbbvezetett ajánlati terv • minden méret mm • helyszínen nem felmért

B–B ALAPRAJZ / VÍZSZINTES METSZET 1:10

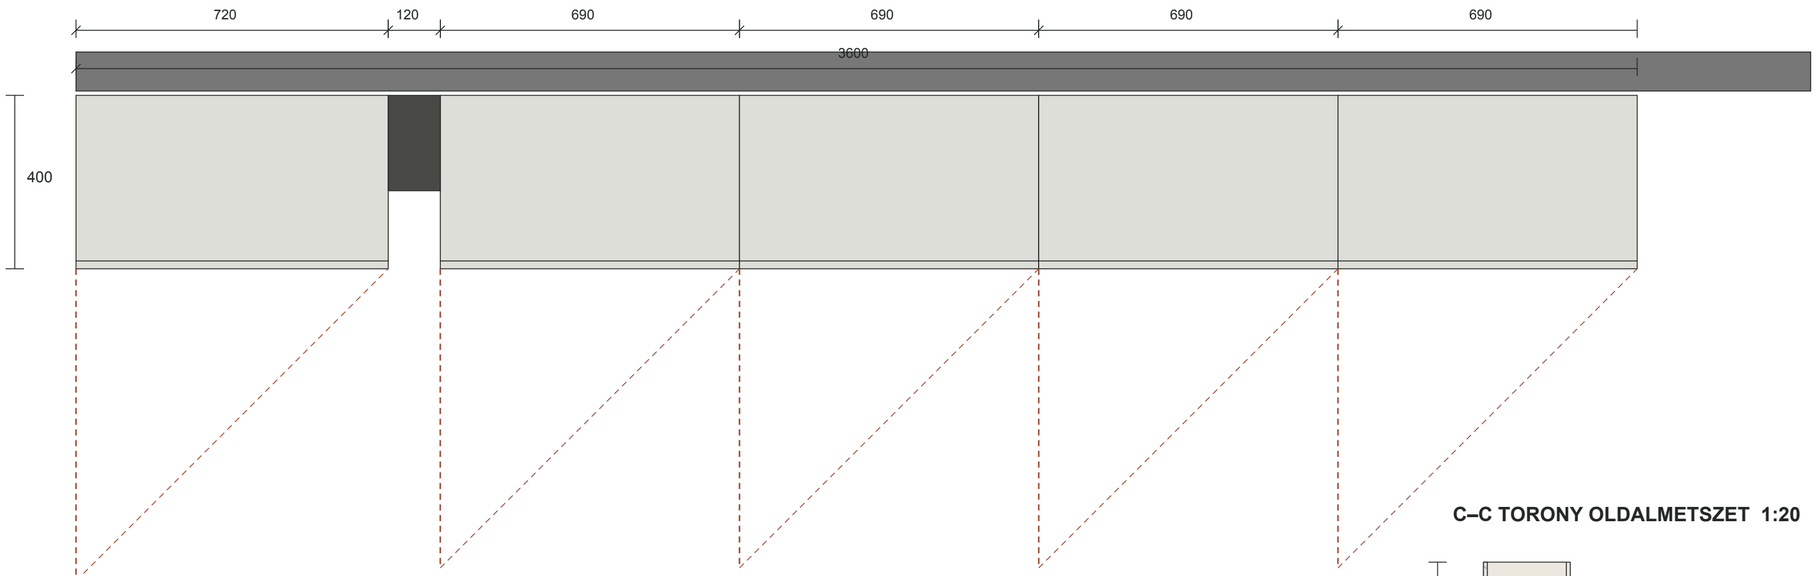

Piros: nyitási helyigény sematikusan; a teljes modulfront sugara720 /690mm.

A rajz helyi bútoralaprajz, nem hitelesített lakásalaprajz. Falsík és falvég felmérendő.

Oldalnézet kivételesen1:20

400mm teljes mélység =382mm korpusz +18mm front.

8mm hátfal süllyesztve / rögzítés gyártói részlettel.

320mm polcmélység: hely marad hátfalhoz és fogáshoz.


Torony külön falrögzítése; nem az alsó lebegő bútorra terheljük.

A statikus/asztalos határozza meg a konzolokat és a csavarokat.

Szállítás:3600mm fedlap1db vagy jóváhagyott illesztés;

lift/forduló ellenőrzés nélkül nem igazolt felhordhatóság.

C–C TORONY OLDALMETSZET 1:20

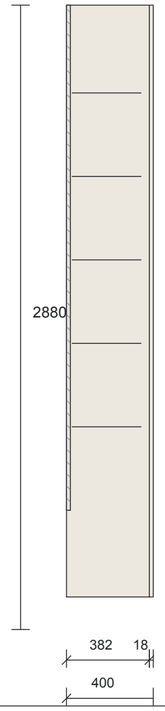

FALHOZ IGAZÍTÁS

A modellfal4000mm; a kompozíció3600mm.300/100mm tervezett végmaradék nem szerelési tűrés. Mérendő3 magasságban szélesség, függő, derékszög, padló és ablakcsatlakozás.

NYITÁSI PRÓBA

Alsó frontok elé690–720mm forgási hely szükséges. A rajz ezt kijelöli, de nem állítja, hogy a kanapé mellett minden front teljesen nyitható. Ha ütközik: vasalatválasztás/oldalirány felülvizsgálat a külső osztás megőrzésével.

FÜGGÖNY

Fali sín Z2840; textil felső él2810, alsó15mm. A redőnyfedélhez hozzáférés és a csatlakozó torony/függöny gyűjtése helyszíni próba. Mennyezeti hűtő-fűtő mezőbe nincs engedélyezett rögzítés.

AJÁNLATKÉRÉSRE / FELMÉRÉSRE VÁR — NEM GYÁRTÁSI KIADÁS

Méretforrás: R10 + geometry_lock_A902_v2b; belsők R11 tervezési javaslat. Nyomat/minta nem jóváhagyott.

2026.10.28. | 1:10 / részletek jelölve


KI-R11 | N-03 | A2 fekvő, 100%-os nyomtatás

WSG A-902 / KYOTO INK

Csomópontok | bonthatóság, fény és grafikai illesztés

R11 • R10 külső geometriából továbbvezetett ajánlati terv • minden méret mm • helyszínen nem felmért

D01 / PANEL RÉTEGREND

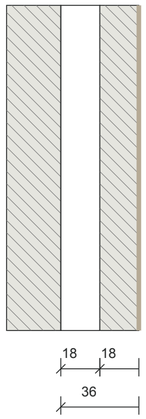

Meglévő fal: helyszíni teher-/anyagvizsgálat.


18mm szerelőlégrés; oldható rejtett függesztés.

18mm stabil hordozólap, matt kasírozott nyomat.

Kábelt nem szabad végleg befalazni / beragasztani.

Felső LED a profilban; nincs önálló világító panelél.

D02 / KÖZTES VISSZAHÚZÁS

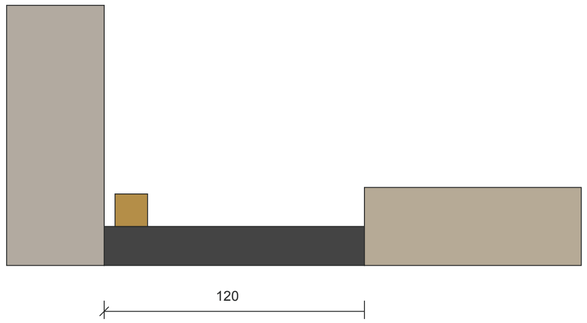

FELÜLNÉZETI ELV

120mm látható sáv,

mélységi lépcső valós.

Oldható hátbetét.


LED profil15mm jelölt;

végleges profiladat kell.

Ragasztott fix takarás tilos

a szervizcsatlakozásnál.

D03 / ALSÓ BÚTOR FÉNYE

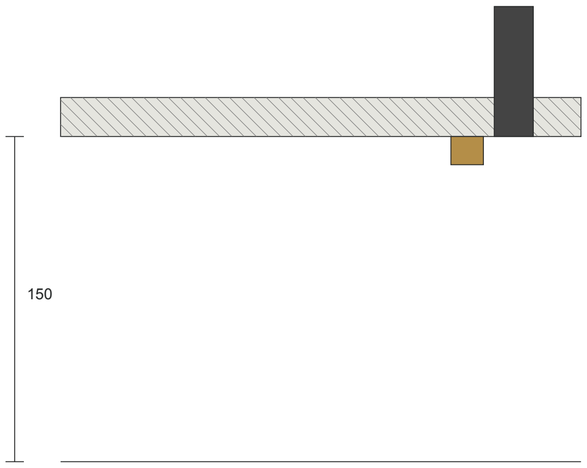

Bútor alsó él150mm a kész padlótól.


Alumínium profil + diffúzor: hőelvezetés.

Tápegység nem az alsó résbe szorítva,

hanem a hozzáférhető AV rekeszben.

Rögzítési méret statikai vizsgálattal.

D04 / FRONT ÉS NYOMAT

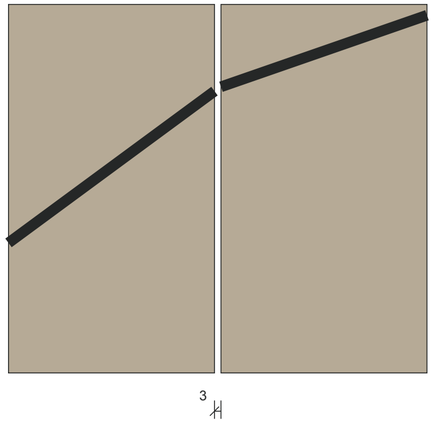

3mm hézag: a grafika megszakad.

Közös masterből kivágott nyomatok.

Élre fordulás / vágás mintázandó.

Fekete oldalél vagy grafit ABS jelölt.

Nyomdai kifutó: gyártó adja meg,

nem a3mm ajtórést kell kitölteni.

AJÁNLATKÉRÉSRE / FELMÉRÉSRE VÁR — NEM GYÁRTÁSI KIADÁS

Méretforrás: R10 + geometry_lock_A902_v2b; belsők R11 tervezési javaslat. Nyomat/minta nem jóváhagyott.

2026.10.28. | 1:2 / sematikus szerelési részletek

KI-R11 | N-04 | A2 fekvő, 100%-os nyomtatás

WSG A-902 / KYOTO INK

Darabjegyzék | előzetes anyagkiírás és vasalatigény

R11 • R10 külső geometriából továbbvezetett ajánlati terv • minden méret mm • helyszínen nem felmért

A táblázat kész alkatrész-befoglalókat ad; élzárás levonása, horony, kötés és nyers szabás gyártói feladat.

Azonosító	Megnevezés	Db	Hossz	Szél.	Vast.	Anyag	Él / megjegyzés
TV01-S	Torony oldalak	2	2330	382	18	M03	elöl1mm
TV01-T	Torony tető/fenék	2	684	382	18	M03	elöl1mm
TV01-C	Torony középosztó	1	2294	374	18	M03	elöl1mm
TV01-P	Torony állítható polc	10	331	320	18	M03	elöl1mm
TV01-F	Torony front	2	2327	357	18	M01+nyomat	körbe1mm
TV01-H	Torony hátlap	1	2294	684	8	M03	nem
TV02-S	Alsó oldalak	10	382	382	18	M03	elöl1mm
TV02-T1	720-as modul fenék	1	684	382	18	M03	elöl1mm
TV02-T2	690-es modul fenék	4	654	382	18	M03	elöl1mm
TV02-P1	720-as modul polc	1	682	320	18	M03	elöl1mm
TV02-P2	690-es modul polc	3	652	320	18	M03	elöl1mm
TV02-F1	Alsó front720	1	717	397	18	M01	körbe1mm
TV02-F2	Alsó front690	4	687	397	18	M01	körbe1mm
TV02-H1	Hátlap720	1	684	346	8	M03	nem
TV02-H2	Hátlap690	4	654	346	8	M03	nem
TV02-CAP	Összefüggő felső fedő	1	3600	400	18	M01	látható1mm
TV03-P	Dekor hordozópanel	4	2330	687	18	M02	mintázandó
GAP	Köztes sáv hátbetét	1	2330	120	18	M01	körbe1mm

Kiválasztott tetőelv:382mm magas oldalak +18mm közös tető =400mm teljes bútor. Fenéklap18mm; tiszta magasság346mm. Nincs külön modultető. A3600mm fedő illesztését és szállíthatóságát gyártó ellenőrizze; a névleges méretek felmérésig nem gyártási adatok.

Vasalat:40db toronypolctartó +16db alsó polctartó, teherbírási jóváhagyással; rögzített tető/fenék kötése gyártói rendszer.

Frontok:2 magas +5 alsó ajtó; pánt/csillapító darabszám gyártói tömeg- és magasságtáblázatból, nem becsült csavarlista.

M01: grafit lap, EGGER U961 ST7 jelölt; M02: nyomathordozó a18mm lapon; M03: világos egyszínű belső laminált lap.

Polcfelület: torony1,059m²; alsó (682+3×652)×320=0,844m². Fenéklap, AV és köztes sáv nélkül.

A becsült1250500Ft asztalos keret új ajánlattal igazolandó. Nem bizonyított, hogy minden új belső részlet ezen belül elkészül.


WSG A-902 / KYOTO INK

CF-01 + ST-01 | grafit asztalok, három nézet és szerkezet


R11 • R10 külső geometriából továbbvezetett ajánlati terv • minden méret mm • helyszínen nem felmért

CF-01 / ZÁRT DOBOZTEST


ELÖLNÉZET

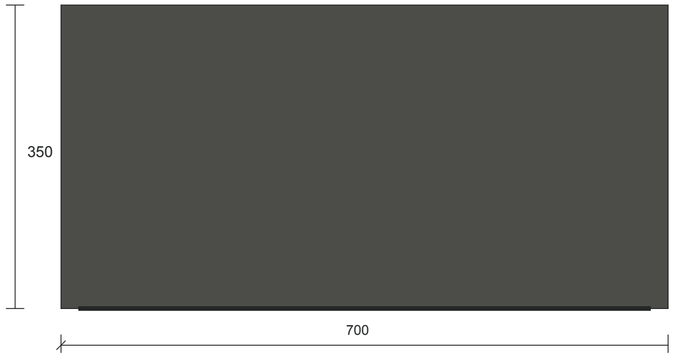

OLDAL

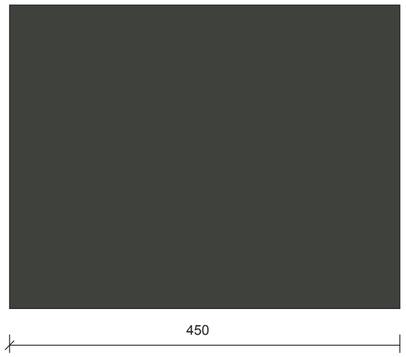

FELÜLNÉZET

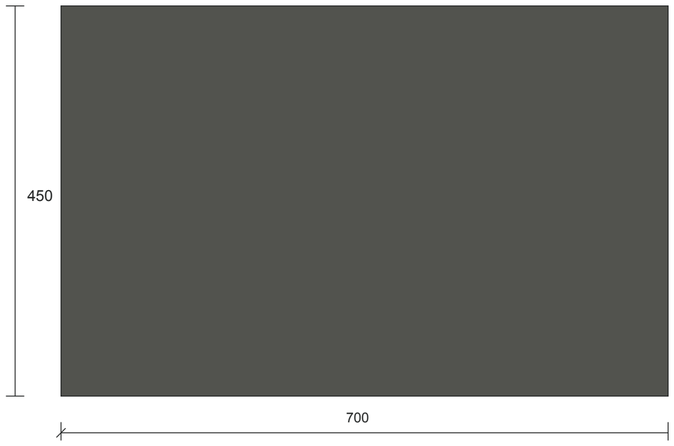

Kész befoglaló700×450×350mm;18mm lap.

Tető1db:700×450; alj1db:664×414.

Hosszoldal2db:700×332; végoldal2db:414×332.


Lapillesztés: zárt doboz, rejtett kötés, körben1mm ABS.

Nem kő / nem valódi tömör fém. M01 grafit mintázandó.

Filctalp padlóvédelem; kész magasságba beleértendő.

ST-01 / ZÁRT DOBOZTEST


ELÖLNÉZET

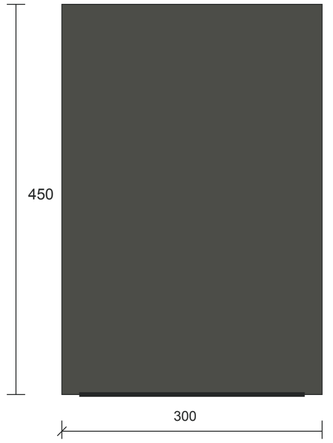

OLDAL



FELÜLNÉZET

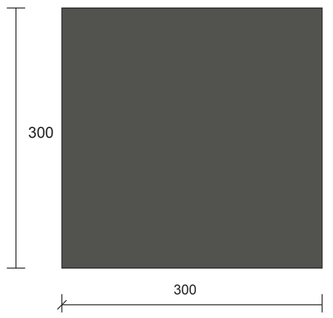

Kész befoglaló300×300×450mm;18mm lap.

Tető1db:300×300; alj1db:264×264.

Hosszoldal2db:300×432; végoldal2db:264×432.

Lapillesztés: zárt doboz, rejtett kötés, körben1mm ABS.

Nem kő / nem valódi tömör fém. M01 grafit mintázandó.

Filctalp padlóvédelem; kész magasságba beleértendő.