
AT8-01 Külön tároló berendezése

Alaprajz + polcnézet · 1:10 A3-on · [J] grafikus tervolvasat; minden kész méret [H]

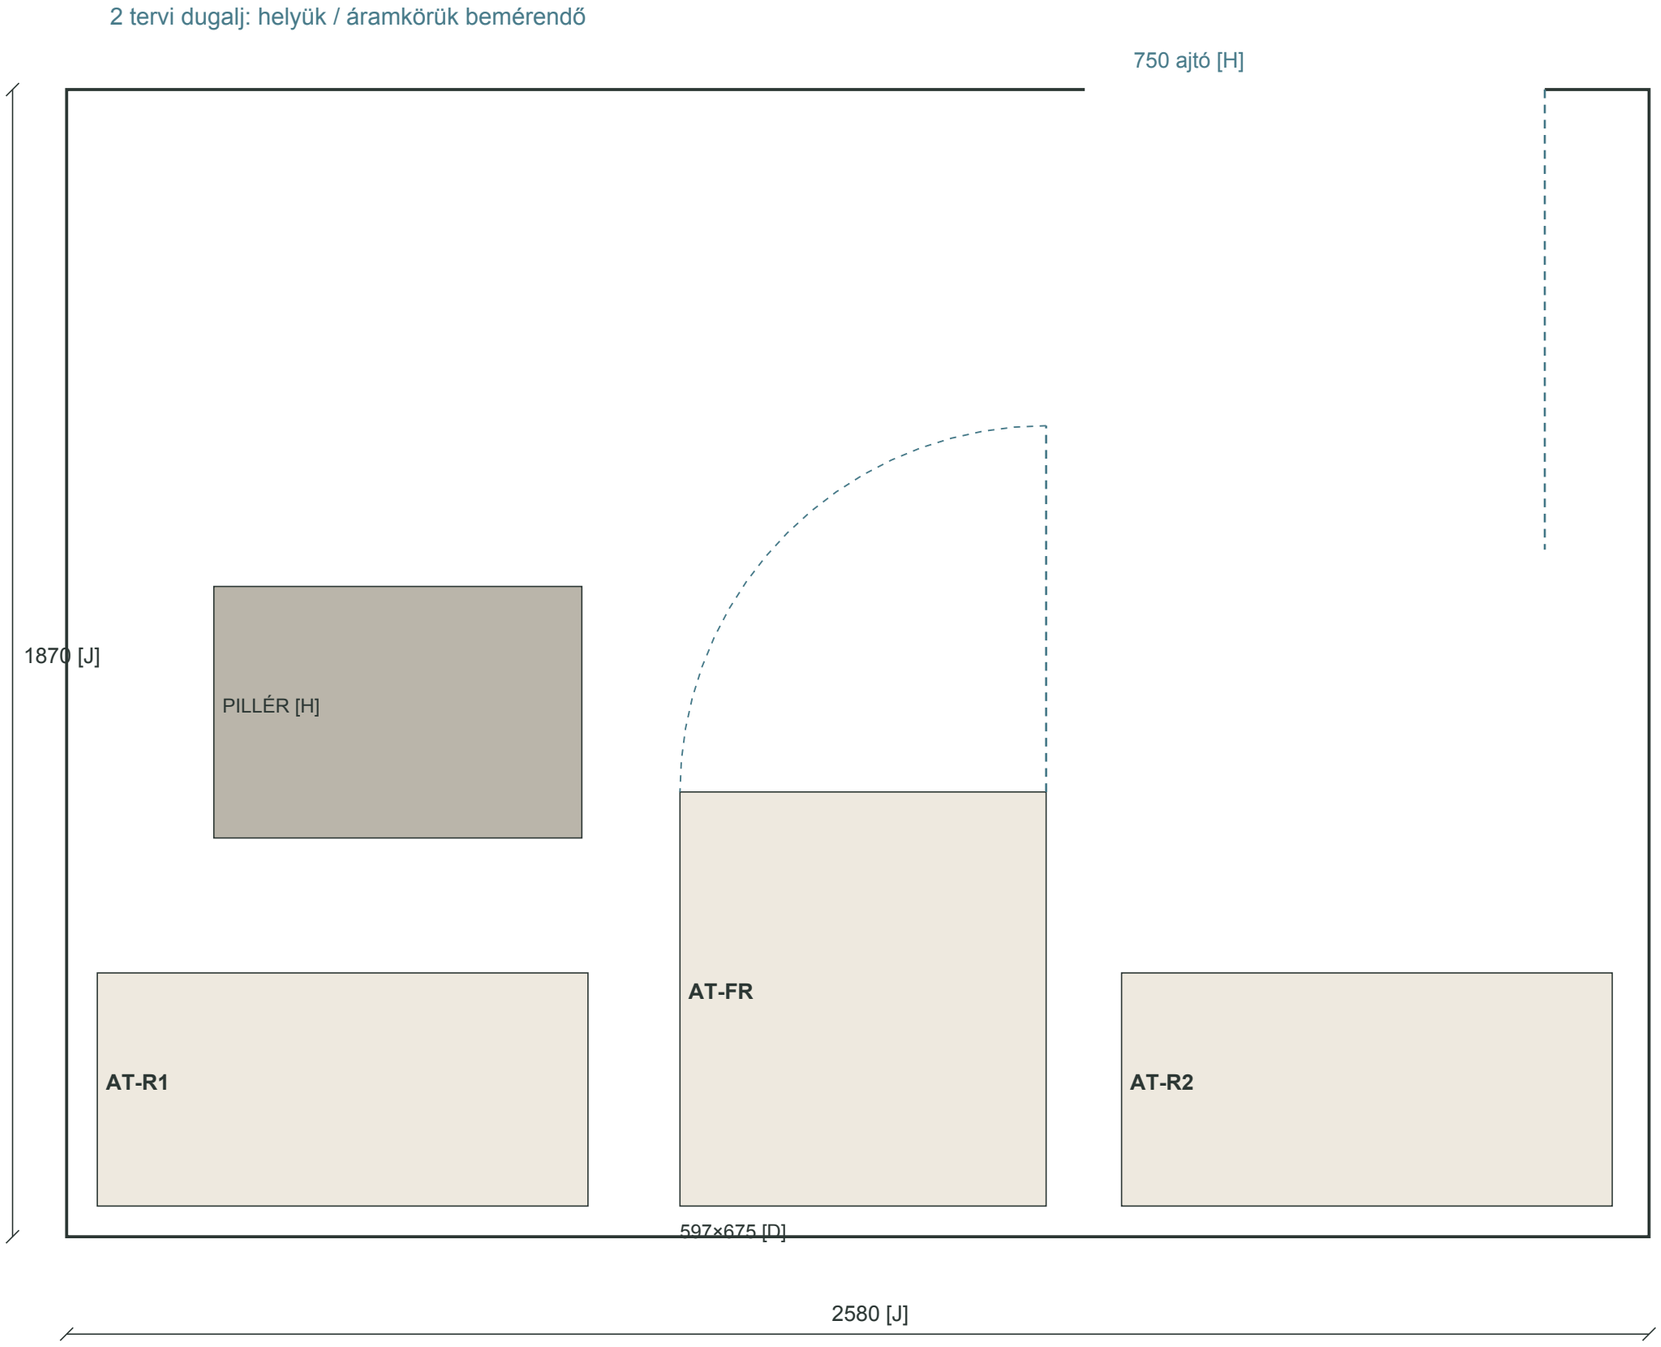

Forrás

WGR1 méretezett alaprajzok: AT8-01 a 2. lap térképi kontúrja és a 26–27. lap 4,57 m² módosítása; T-0-26 a 4. lap 4,00 m² helyisége. A grafikai leolvasat nem kész belméret.

Fontos eltérés

AT8-01 régebbi villamos rajza még a korábbi kontúrt mutatja. A két dugalj tervi tény; az ottani falhossz nem került át automatikusan.

Bútorok

2× JONAXEL fehér 800×380×1600; 4 polcszint, 25 kg/polc; köztük 597×675×1455 fagyasztó.

Használat

Nehéz készlet alul, élelmiszer zárt dobozban. A fagyasztó szellőzési és ajtónyitási gyári távolsága az EAN-azonosítás után ellenőrizendő.


Magasság

2400 mm csak jelenetbefoglaló. Nem a lakás 2900 mm-es magasságának átvétele.

Költség


KI-CP3-S01–S04; fagyasztó külön F01/F02. Szerelés, dobozok és falrögzítés is szerepelnek.

Készpolc elvi nézete; polcállások a készlettel.

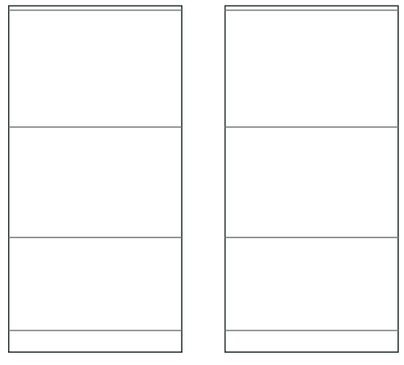

T-0-26 Külön tároló berendezése

Alaprajz + polcnézet · 1:10 A3-on · [J] grafikus tervolvasat; minden kész méret [H]

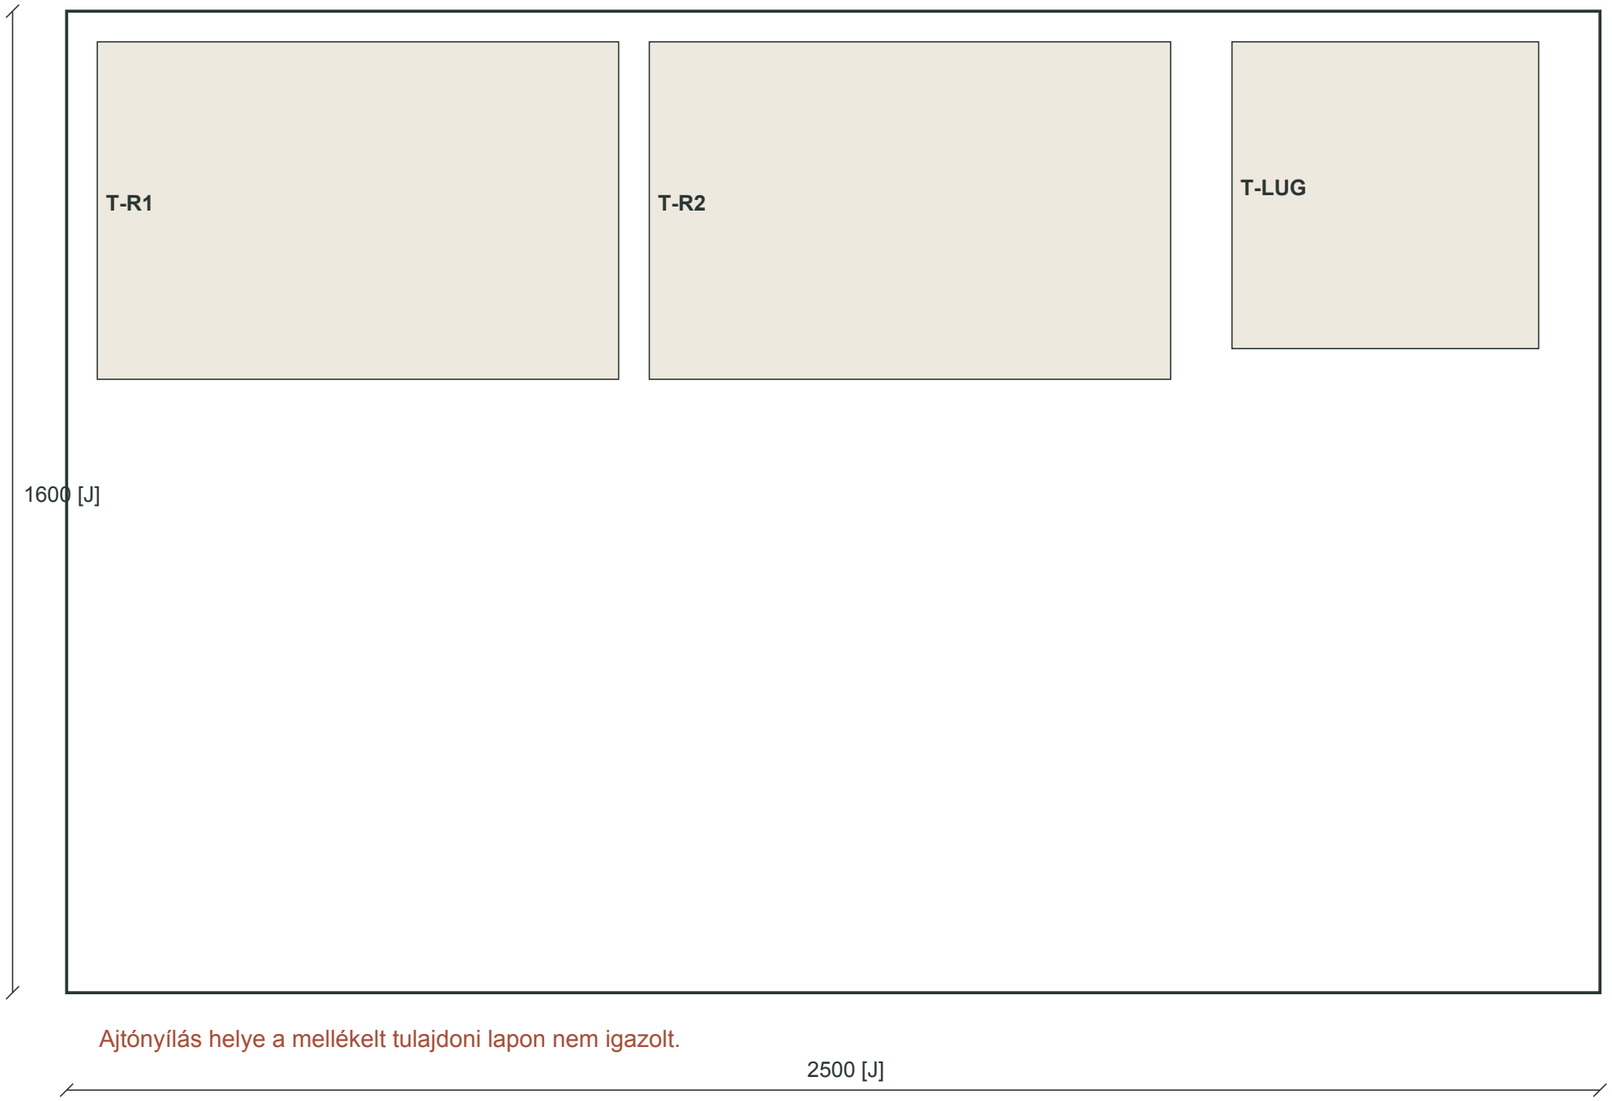

Forrás

WGR1 méretezett alaprajzok: AT8-01 a 2. lap térképi kontúrja és a 26–27. lap 4,57 m² módosítása; T-0-26 a 4. lap 4,00 m² helyisége. A grafikai leolvasat nem kész belméret.

Fontos eltérés

A 2500×1600 mm feltételes elrendezési keret. Ajtó, belmagasság és falvastagság helyszíni felmérés előtt nem igazolt.

Bútorok

2× BROR fekete 850×550×1900; állítható polc; további 500×500 padlóhely bőröndnek. Teher a konkrét készlet gyártói adatával.

Használat

Ritkán használt nagy tárgyak; a napi gardróbok nem csökkentek emiatt. Rögzítés és nedvességi viszonyok ellenőrizendők.


Magasság

2400 mm csak jelenetbefoglaló. Nem a lakás 2900 mm-es magasságának átvétele.

Költség

KI-CP3-S01–S04; fagyasztó külön F01/F02. Szerelés, dobozok és falrögzítés is szerepelnek.

Készpolc elvi nézete; polcállások a készlettel.

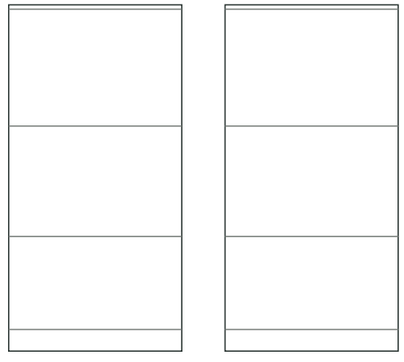

P-CP3 Teljes lakás - tárolás és belső fény

Tervi elhelyezés és azonosítók · 1:50 A3-on · Kiállások végleges helye felmérésre vár




Arany jel: belső fénycsoport. A 73 lámpa / 13 tápegység pontos rekesz- és áramköri csoportja a CP3 belső fény és tápegység munkalapon. A vezeték a korpusz oldalsó csatornájában fut, nem a nyitófronton. Dugaljhely nincs helyszíni bizonyíték nélkül újként rárajzolva.

K-CP3 / ST lapok: külön használati korlátok. A két külső tároló külön koordinátatérben van; nem a lakás szobájaként számított terület.

K-CP3 Konyhai működés és kamra-alternatívák

Meglévő gép- és vízhelyek megőrzésével · 1:10 részlet · 840 mm munkaköz nyitott korlát

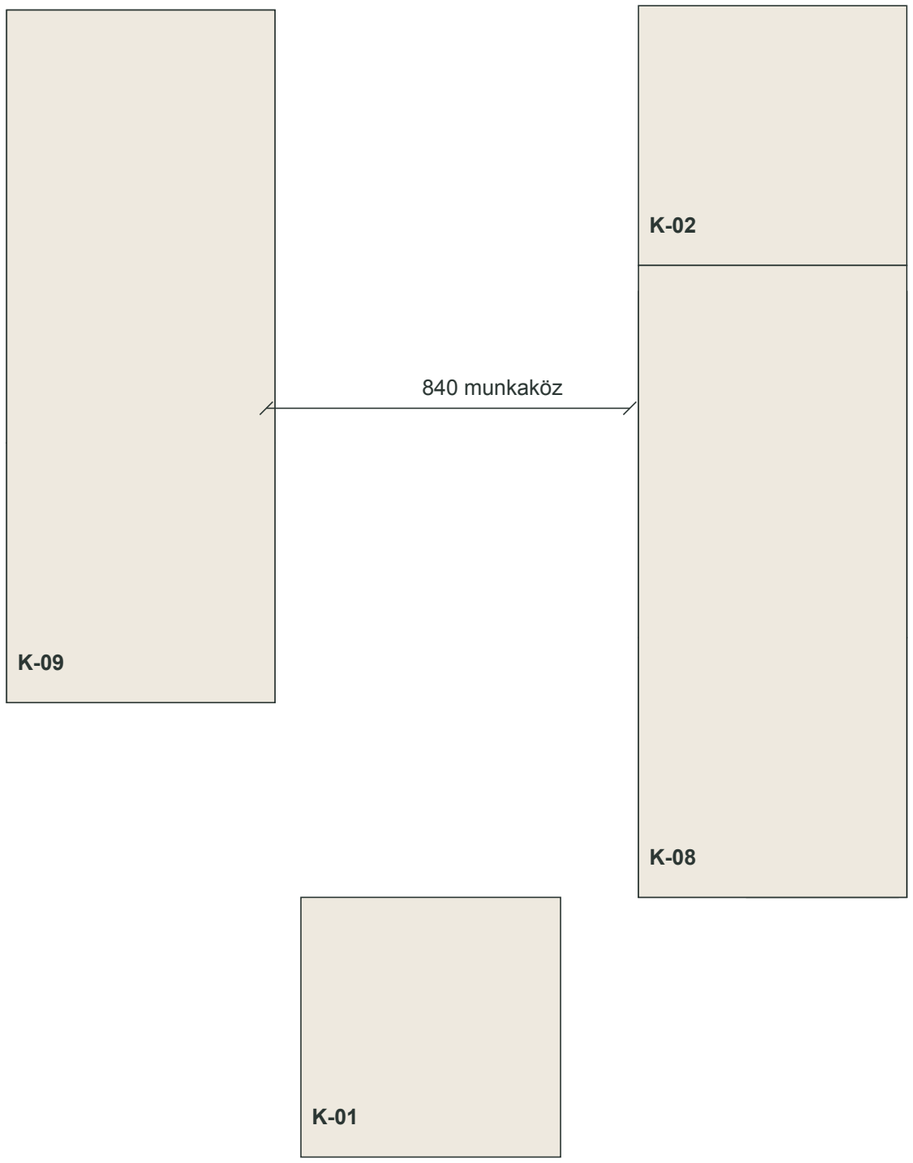

Használati sorrend

Hűtő K-02 → mosogató melletti kis lerakó → K-03 mosogató → átfordulás K-06 nagy előkészítőhöz → K-05 főzőlap → edénylerakó a szomszéd pulton → K-01 sütő/mikro. Többsoros konyha; nem egyetlen balról jobbra nézet.

Napi gépek

K-04 mosogatógép fölötti kb. 600 mm pult a kávé/pirító zónája. A felnyíló gépfedelek és felső szekrény közti távolság géptípus alapján ellenőrzendő. K-06 marad az előkészítésé.

Lerakó feltétel

A mosogató pontos mérete még hiányzik; a hűtő felőli kb. 300 mm lerakó csak kompakt medence és gyártói kivágás mellett alakítható ki. Nem igazolt, kész munkapultként nem számított.

Kamra A - 800 mm

800×600×2400, két 400 mm ajtó; öt belső fiók; felső bortartó és polcok. 420 000 Ft becsült teljes új elem, kiváltott K-06-rész után nettó felár ajánlattal. A 1000 mm előkészítő 200 mm-re fogy: nem javasolt fővváltozat.

Kamra B - 300 mm

300×600×2400 keskeny kihúzható; 5 kosár. 160 000 Ft becsült új elem, kiváltott korpusz levonandó. 700 mm előkészítő marad: érdemi kompromisszum, nem automatikusan elfogadott.


Fő javaslat

K-01 felső szárazélelmiszer, K-07 napi készlet, K-06 alsó fiókok; ritka nehéz gép alul.
AT8-01 csak tartalékkészlet. A kért teljes kamra még nem fér be tartalomveszteség nélkül.


KP-800 / KP-300 Kamraszekrény alternatívák

Külön javaslatok, nem főváltozat · mm · 1:15 A3-on · Elhelyezés / költség jóváhagyásra vár

KÉTAJTÓS

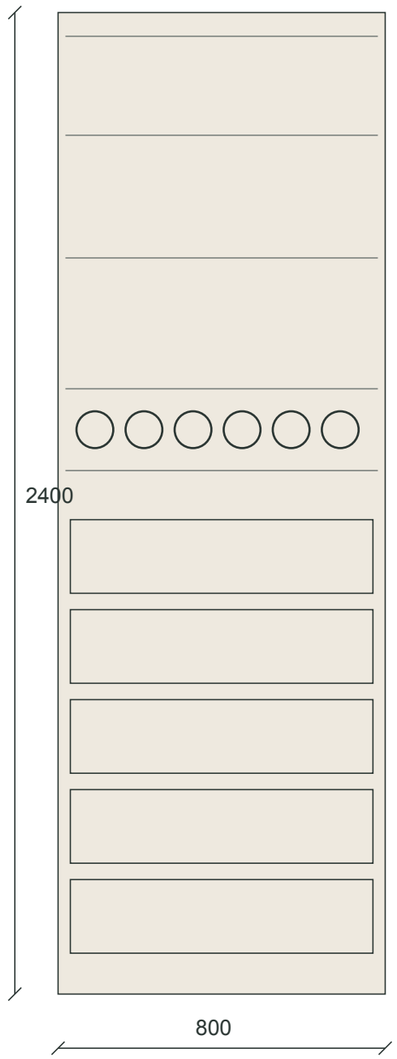

KIHÚZHATÓ

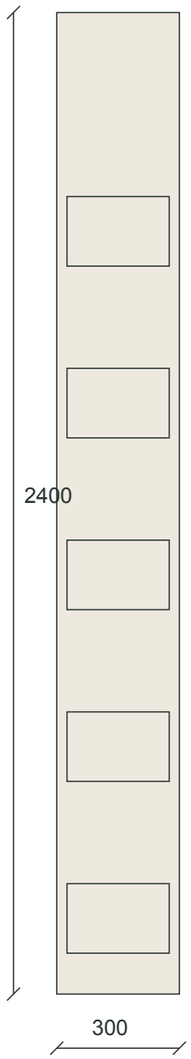

KP-800 szerkezet

18 mm korpusz, 19 mm matt front, 8 mm hát, 30 mm szerviz; 764 mm nettó belszélesség. 5× 664×400×150 mm tervezett fiók: 199,2 l. 155° nulla-benyúlású pánt; 450 mm vezető. Belső fiókok és ajtók együtt próbálandók.

Ajtóbelső tároló

75 mm mély tea/fűszer kosarak csak a felső, fiókok fölötti ajtózónában: 1250–2000 mm. Nem a fiókok elé. A boros rész 330 mm mély, a palackhossz felmérendő. 6 palackos egy sor a rajzon; nem borhűtő.

KP-300 szerkezet

264 mm névleges belszélesség; kosár tényleges nettó mérete és a magas kihúzó terhelése konkrét vasalattól függ. 5 kosár 420 mm raszteren. Nem jelöltük 100%-ban kihasználható tömör térfogatként.

Fény és szerviz


KP-800 felső és fiókos rész frontközeli 24 V fénye; ajtóérzékelő, felső hozzáférhető meghajtó. KP-300 oldalsó profil, mozgó kosárszerkezet útján kívül. Fénykészlet és bekötés a kamra árajánlatának része.

Döntés

A rajzok tényleges alternatíva-kialakítások. A 840 mm munkaköz és az elvesző pult miatt nem kerültek észrevétlenül a fő lakásmodellbe vagy a költségösszegbe.

B62-CP3 Hajápoló fiók és villamos szerviz

900×500×350 mm célbefoglaló · mm · 1:5 részlet · Vizes zóna és gyártói jóváhagyás szükséges

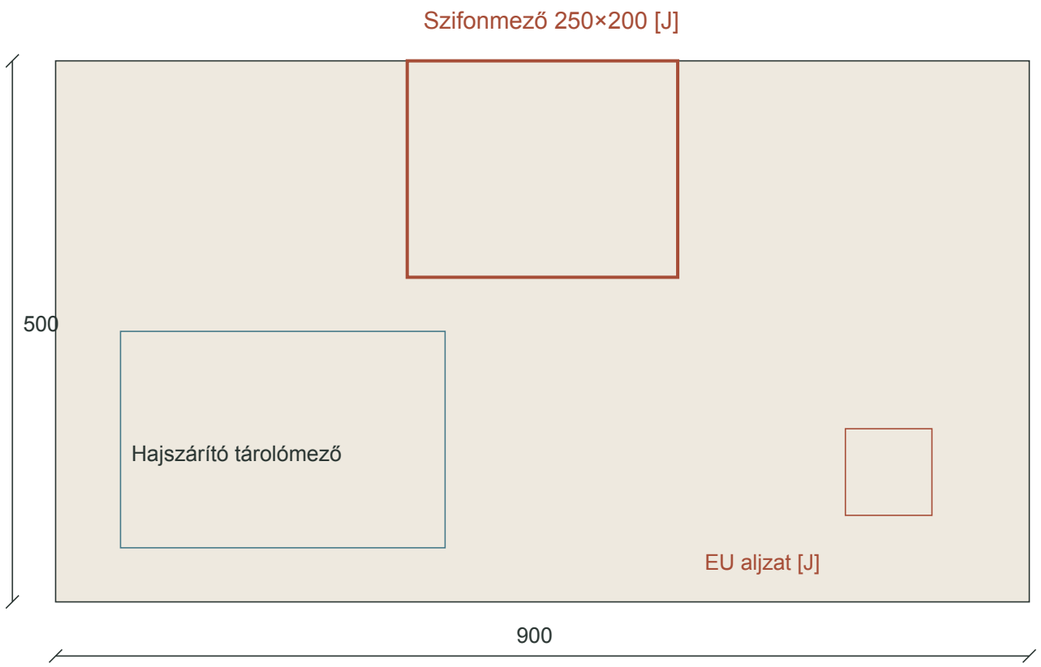

Metszeti elv: 19 mm front + 450 mm névleges vezető + 8 mm hát = 477 mm. A fennmaradó 23 mm nem automatikus szerelési megfelelés: a konkrét vasalat előírt korpuszmélysége és a vízcsatlakozás dönt. A rajz nem engedélyezi a mosdókerámia vágását.

Fiókkialakítás

Felső fiók U alakú szifonkikerüléssel; alsó fiókban elkülönített hajszárító és tartozék. 450 mm névleges vezető tervezett. A 30 mm hátsó szervizsáv itt elmarad: kábel a felső / oldalsó hozzáférhető térben.

Jelölt rendszer

Blum AMPEROS AC, EU 230 V, ESS.B01FA.2 jelölt aljzat. Nem amerikai 120 V termék. Pontos 450 mm vezetőhöz tartozó kábelvezetés, kompatibilis fiókrendszer és rendelési lista gyártói egyeztetésre vár.

Bekötés

Meglévő, bemért kör → villanyszerelő által ellenőrzött védelem → fix bútorcsatlakozás → gyári mozgó kábelvezető → fiókaljzat. Laza hosszabbító és éles élen megtört kábel nincs a tervben.

Használat


Forró hajformázó nem zárható textilre. Használat nyitott fióknál, száraz kézzel; tárolás kihűlve, áramtalanítva. Kapcsolás / hővédelem és a készülék gyártói előírása a végleges szakági terv része.

Kapu / alternatíva

A fiókba integrált rendszer nem jóváhagyott. Ha nem fér el vagy a vizes zóna nem engedi: külön, hozzáférhető fix aljzat, ugyanazzal a tárolórekesszel. Fő előirányzat 145 000, gazdaságos fix megoldás 40 000 Ft; nem egyszerre összegezve.

05.2 Gyerek / gardrób: változtatható napi tér

Összehasonlító alaprajz · 1:20 A3-on · Tulajdonosi döntésre váró alternatíva, nem kiválasztott fővátozat

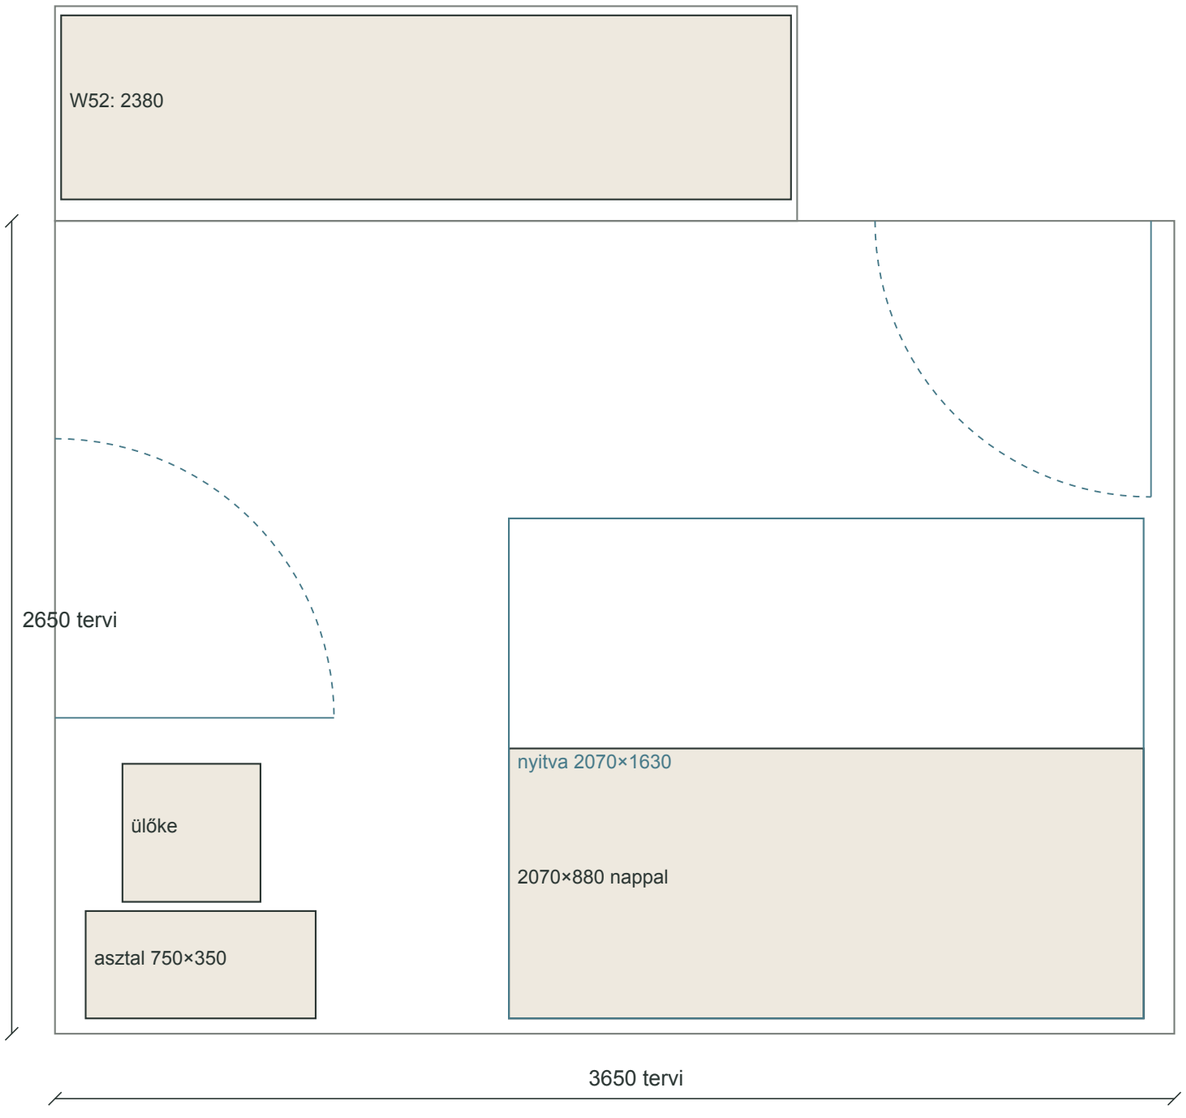

Megőrzött kapacitás

W52 változatlan: 1,437 m akasztás, 4,250 m² polc, 123,9 liter fiók; 1 gardróblift. Nem veszünk el szekrényt az ajtóütközés miatt.

A: meglévő ágy + kompakt asztal

A fő ágy helyén marad. ALT052_B: 750×350 mm lehajtható lap és 450×450 mm ülőke; az erkélyajtó mintavételezett nyitási próbája megfelelt. A lap magassága és a szék a gyerek korához igazítandó. Nem teljes felnőtt munkaállomás.

B: nappali / alvó átalakítás

FYRESDAL 204.243.62 fekete acél jelölt: 2070×880×940; nyitva 1630 mm széles, két 800×2000 matraccal. A rajzon nappali és éjszakai helyigény. A két állapot között 1,55 m² padló szabadul fel; ez nem új szobaterület.

Ár és látvány

Magyar ár/szállítás nincs igazolva; a finn oldalon kifutó jelölés. 180–260 ezer Ft komplett helyettesítési előirányzat, nem bekerült projektköltség. Nettó csereár az aktuális ágy+matrac+szállítás kiváltása után számítható. A fekete fém sziluett eltér a kárpitozott Kyoto Ink ágytól.

Modularitás és ellenőrzés


A gardrób rögzített külső mérete mellett 32 mm-es polcraszter, kivehető játékdobozok, cserélhető belső polcok. Gyerekbiztonság, kor, ablak- és függönyhely, asztalrögzítés és a nyitható ágy teljes mozgása még ellenőrzendő.

Forrás

IKEA Finland / FYRESDAL20424362, 2026-10-27. A B alternatíva méretezett tervi elhelyezés, nincs Blender PASS-ként kiadva.

05.3 Vendég / munka: azonos időben használható funkciók

Összehasonlító alaprajz · 1:20 A3-on · Tulajdonosi döntésre váró alternatíva, nem kiválasztott fővváltozat

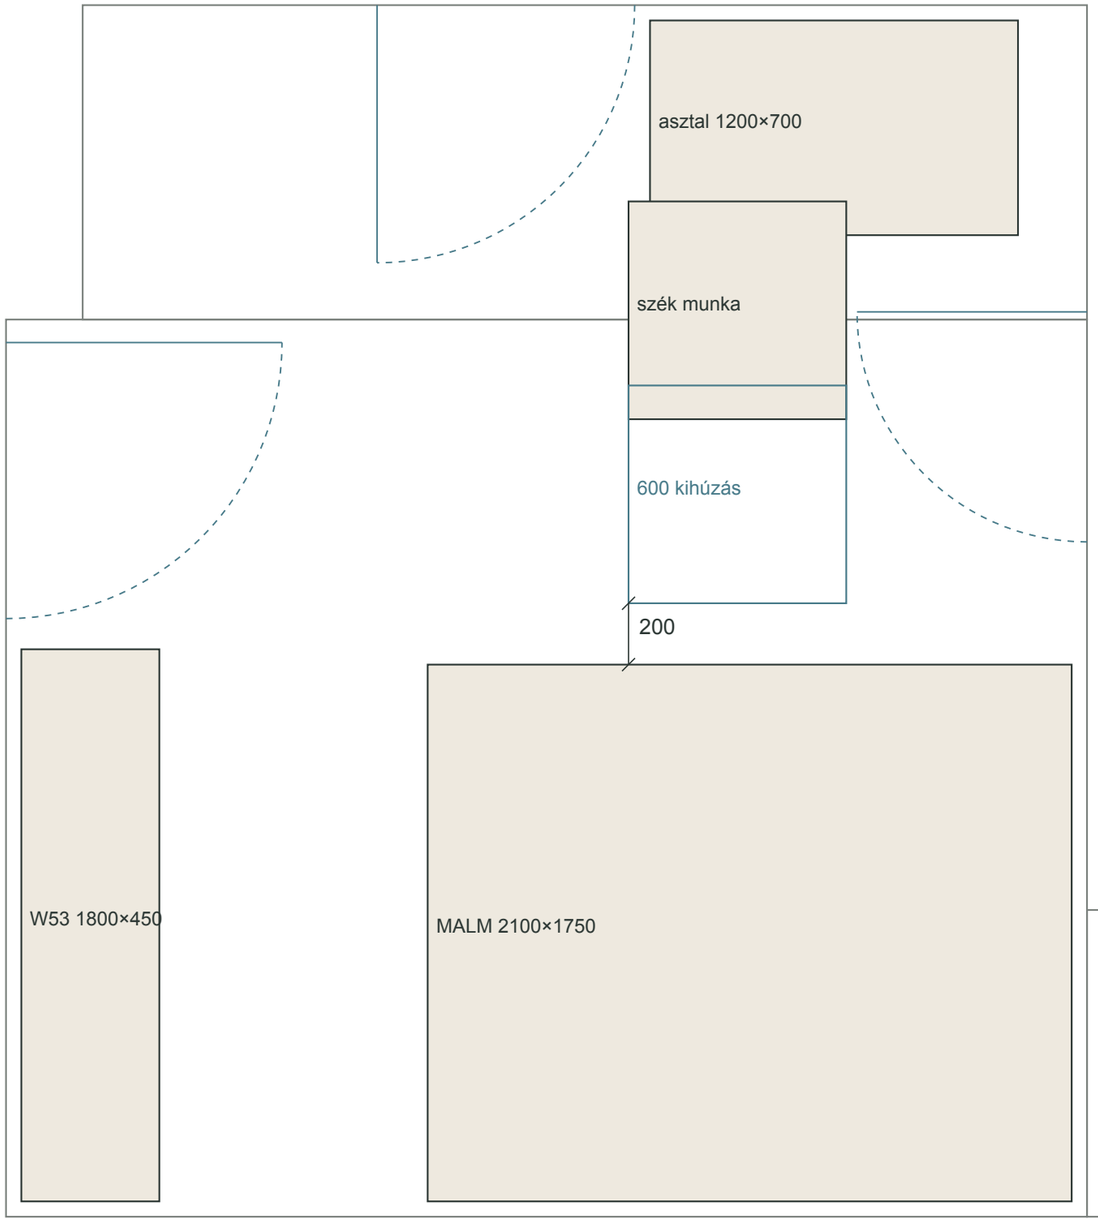

Fővváltozat hibája

NORDLI180 + jelenlegi munkaszék: 600 mm kihúzásnál 100 mm átfedés az ágy befoglalójával. Ezért a fővváltozat nem kapott megfelelt státuszt.

Kidolgozott ALT053

MALM 204.048.06 fehér, 160×200 matrac; gyári befoglaló 2100×1750×1000. Az ágy és a széktér között 200 mm elválasztás marad. Ez nem külön közlekedősáv; a megközelítés nyugatról történik.

Futott vizsgálat

A szoba-, fürdő- és teraszajtó 2 fokonként / 100 sugárponttal vizsgált nyitása a négy berendezési befoglalóra megfelelt. A felemelt ágy, nyitott gardrób és valódi székalkatrészek vizsgálata még hiányzik.

Kapacitás és ár

W53 érintetlen: 0,350 m előre húzható rúd, 3,103 m² polc, 83,5 l fiók. Ágykeret 219 900 Ft a korábbi189 900 helyett: +30 000 Ft. A 160-as matrac pontos ára és szállítás külön tisztázandó, nem nulla.

Kompromisszum

A fekvőfelület 20 cm-rel keskenyebb; oldalfiókok helyett felnyíló ágyneműtartó. Világos sima front, eltérő fejvég. Az alternatíva nincs automatikusan kiválasztva az Excelben vagy a fő rendernézetekben.

Forrás

IKEA HU MALM20404806, 2026-10-27; forrásgeometria v2b; CP3 ALT053 kollekció és checks.json. Kész méret és matractömeg gyártói kapu.