
# K-08  Munkalapok és hátfal

01 · Belső kiosztás / metszet · 1:10 A3-on · Ajánlati és felmérési terv

### NYITOTT ELÖLNÉZET

### A-A METSZET

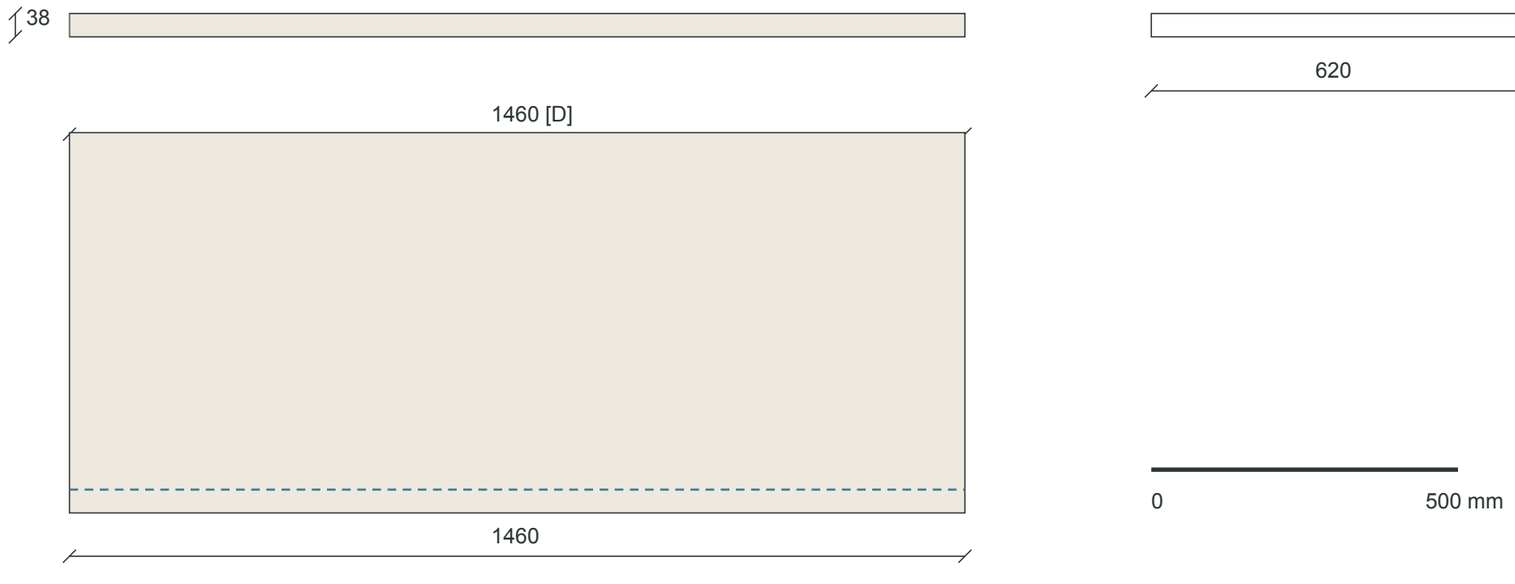


Hátsó 30 mm kábel/szerviz előirányzat + 8 mm hát. Fiók nettó méret nem gyártási szabásképlet.

**Elhelyezés**

x 9.930 / y 1.970 / z 0.900 m; nyitás none

**Méretforrás**

geometry_lock_A902_v2b: terv szerinti falsíkok + R02 tervezési méret; helyszínen nem mért

**Szerkezet**

18 mm laminált korpusz; 19 mm MDF front; 8 mm hátlap

**Felület / él**

F274 betonhatás; látható él 2 mm ABS, belső él 1 mm; vizes élek PUR/gyártói vízzárás

**Vasalat**

Nincs szekrénypánt. Panel: rejtett mechanikus sín, biztosított leakasztás; rögzítési alap és teher ellenőrzendő.

**Fény**

Nem zárt tároló: külön belső fény nem érintett. Kapcsolódó dekorfény az R02 világítási tervben.

**Költségkód**

KI-011, KI-012, KI-014


# K-08  Működés, rekeszméretek és kapcsolatok

02 · Zárt front / használat / részlet · [J] tervezett kialakítás; gyártásra még nem jóváhagyott

### ZÁRT FRONT - V3.3 osztások megtartásával



### HASZNÁLATI / SZERVIZRÉSZLET

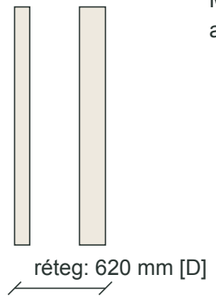


Mechanikus függesztősín és levehető mező; nyomatot a panel- és ajtórésekre bontani. Elektromos szervizfedél nem ragasztható le.

Fényút: helyiségi betáp [H] → hozzáférhető tápegység → oldalsó kábelcsatorna → polc alatti frontközeli fény. A tápegység nem kerülhet takart ruhakupac mögé.

| Rekesz / funkció | Nettó Sz×Mé mm | Polc felső síkja mm | Rúd / lift mm | Fiók belső mm / db |
|---|---|---|---|---|

Keleti pult névleges 1460 + nyugati 1600 mm: külön darabok; 38 mm laminált F274 dekorcsalád, pontos felület mintáról. A rajz befoglaló anyagvizsgálat, a hűtőt nem fedi pult. Nettó pult 1.897 m², rendelés 2.18 m² (15%). Hátfal 1.4×0.55=0.77 m² + végek; nyitott elszívóút.

### Kapacitás [J]: 0.000 m akasztás · 0.000 m² polc · 0.0 liter fiók

A nettó értékekből további 25% szabad tartalék javasolt. Terhelés, nyitási ütközés, fali rögzítés és kész belméret jóváhagyása még szükséges. A részletes alkatrész- és vasalatjegyzék az elemkódhoz kapcsolva.